
HALVBÅGE, SIDA (sett från husets insida) 1:15

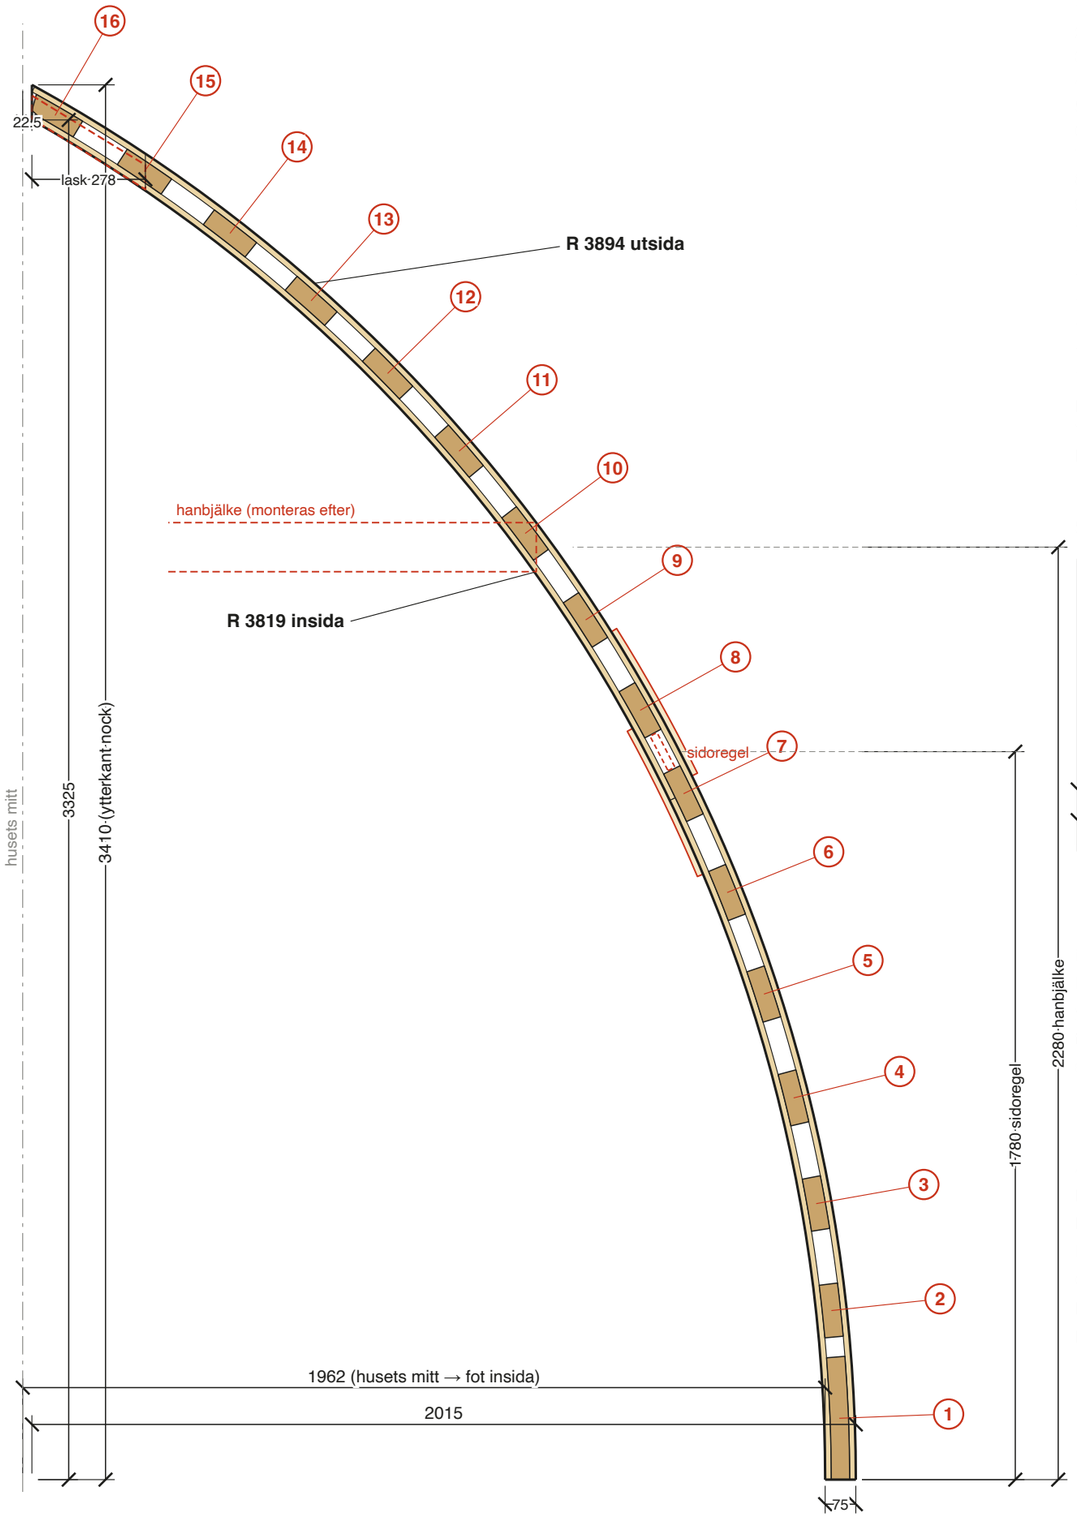


Cirkelns centrum: 1856 bortom husets mitt, i fotens nivå (andra halvans sida).

KLOSSAR – läge mätt längs YTTERKANTEN från foten (måttband på bågen)

nr	typ	längd	från	till	insida från	insida till
1	fot	300	0	303	0	297
2	kloss	130	353	484	346	475
3	kloss	130	619	751	607	736
4	kloss	130	886	1017	869	998
5	kloss	130	1153	1284	1131	1259
6	kloss	130	1420	1551	1392	1521
7	fack	130	1686	1818	1654	1783
8	fack	130	1919	2050	1882	2010
9	kloss	130	2179	2311	2137	2266
10	kloss (hanbj.)	130	2440	2571	2393	2522
11	kloss	130	2700	2832	2648	2777
12	kloss	130	2961	3092	2904	3033
13	kloss	130	3222	3353	3160	3288
14	kloss	130	3482	3614	3415	3544
15	kloss	130	3743	3874	3671	3800
16	nock	130	4004	4135	3926	4055


Fack för sidoregel 19×95 mellan fackklossarna = 100 fritt (2.5 spel/sida).
Ytterkant fot → nock ≈ 4156, insida ≈ 4034. Klossar c/c ≈ 264 nedre / 258 övre.
Nockklossens övre ände kapas lodrätt med flänsarna.

SNITT A-A (genom kloss) 1:2

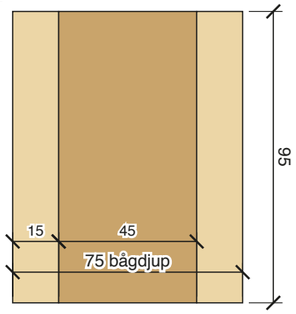

innerfläns 1 × 15 × 95 plywood
kloss regel 45×95 (45 radiellt, 95 tvärs bågen)
ytterfläns 1 × 15 × 95 plywood
flänsarna böjs runt klossarna: lim + 2 skruv 5×60 per fläns och kloss
skarv: en per fläns, mitt på en fackkloss + lask 400 (blad 3)

HEL BÅGE (2 halvor) 1:50

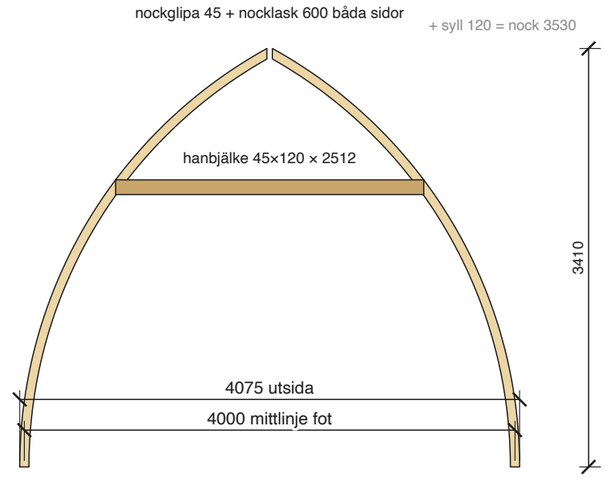

ANMÄRKNINGAR

Foten kapas vågrätt, nocken lodrätt. Flänsarna kapas med 25 mm övermått i ändarna och putsas efter montering.
Hanbjälke: bultas M10 genom kloss 10. OBS med 15 mm fläns och lodrätt kapad ände överlappar
hanbjälken bara innerflänsen – förslag: kapa änden snett längs bågen och lägg den mitt på kloss 10 (se tråden).
Gavelbågar (4 halvor): ingen hanbjälke, nocklask bara på insidan.
Röd streckad = monteras senare (sidoregel, hanbjälke, nocklask). Röd heldragen = skarvlask.
Kontroll: två halvor ihop = 4000 c/c fot (mittlinjen), utsida 4075.

HALVBÅGE – FÄRDIG

18 st (2 per båge). Fläns 1 × 15 plywood, klossar regel 45×95.

Växthus buttercup · båge 1×15 · mått i mm · blad 1/3