



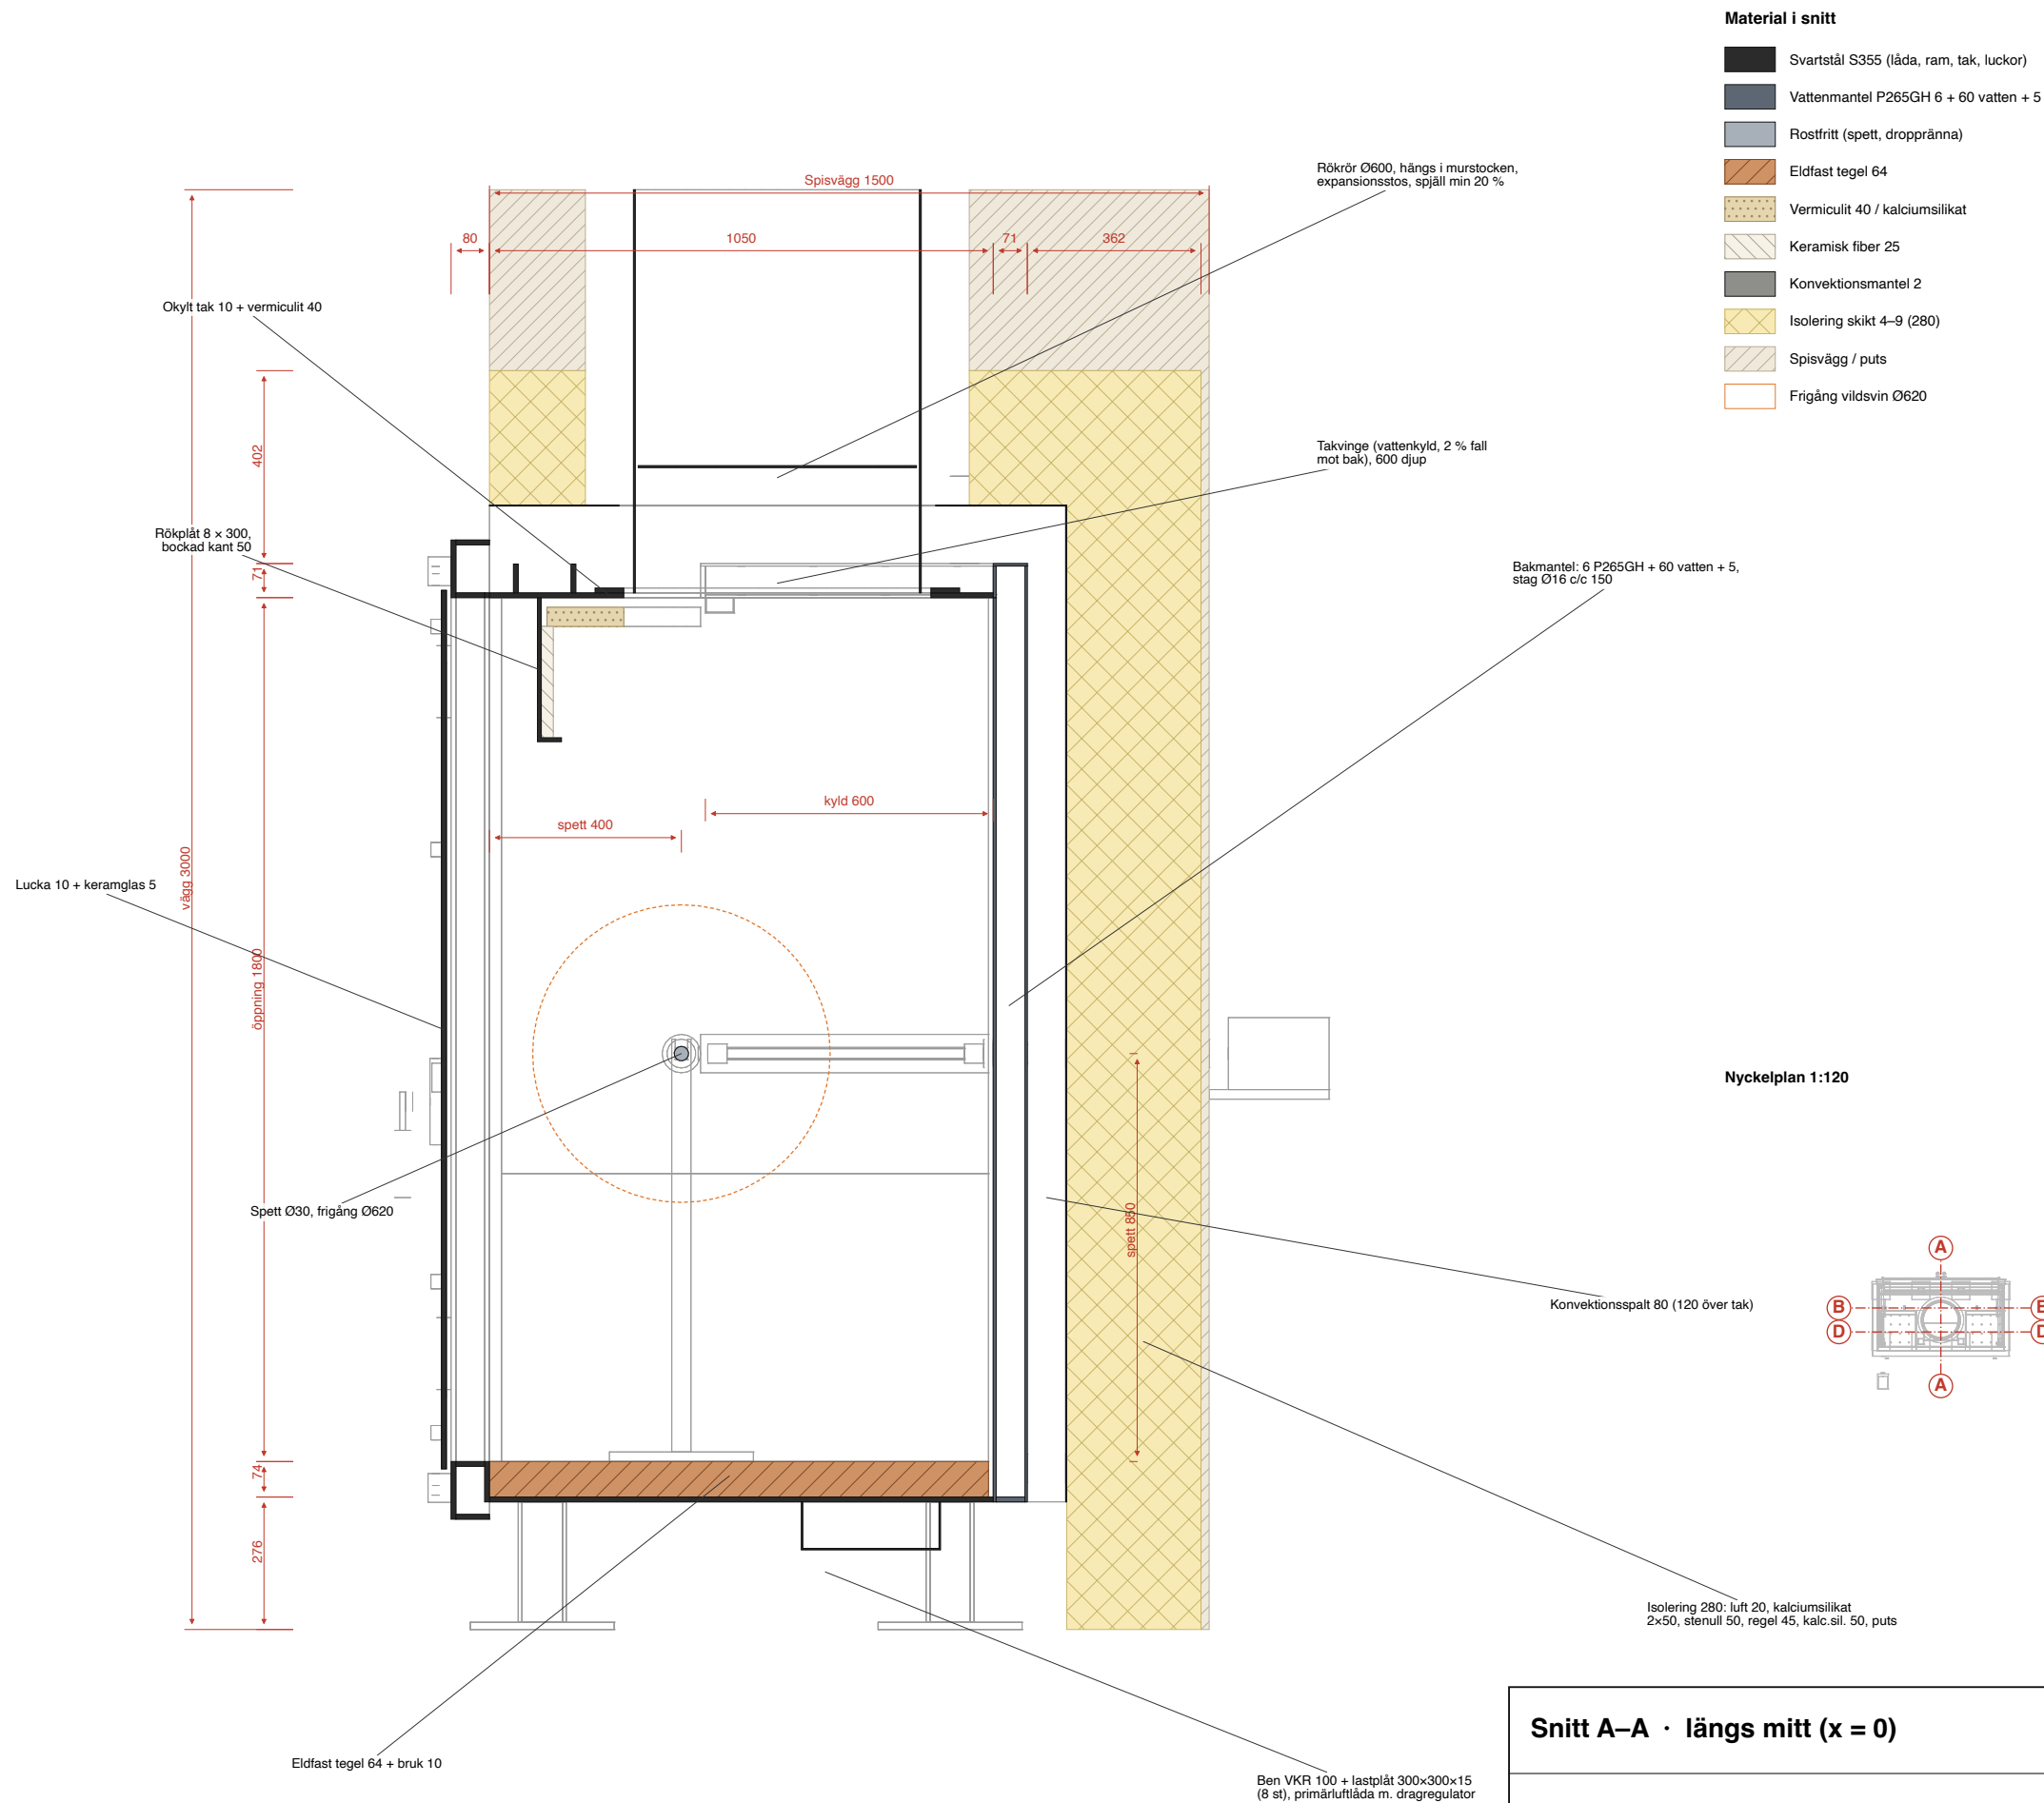


Snitt A–A · längs mitt (x = 0)		
Eldstadsinsats v3 · vattenmantlad bakvägg + takvingar		Skala 1:15 (A3)
Garibaldi · Hugo Ljungberg · 2026-10-10 · mm		Blad 1 / 6

- Svartstål S355 (låda, ram, tak, luckor)
- Vattenmantel P265GH 6 + 60 vatten + 5
- Rostfritt (spett, droppränna)
- Eldfast tegel 64
- Vermiculit 40 / kalciumsilikat
- Keramisk fiber 25
- Konvektionsmantel 2
- Isolering skikt 4–9 (280)
- Spisvägg / puts
- Frigång vildsvin Ø620

B–B genom spettet

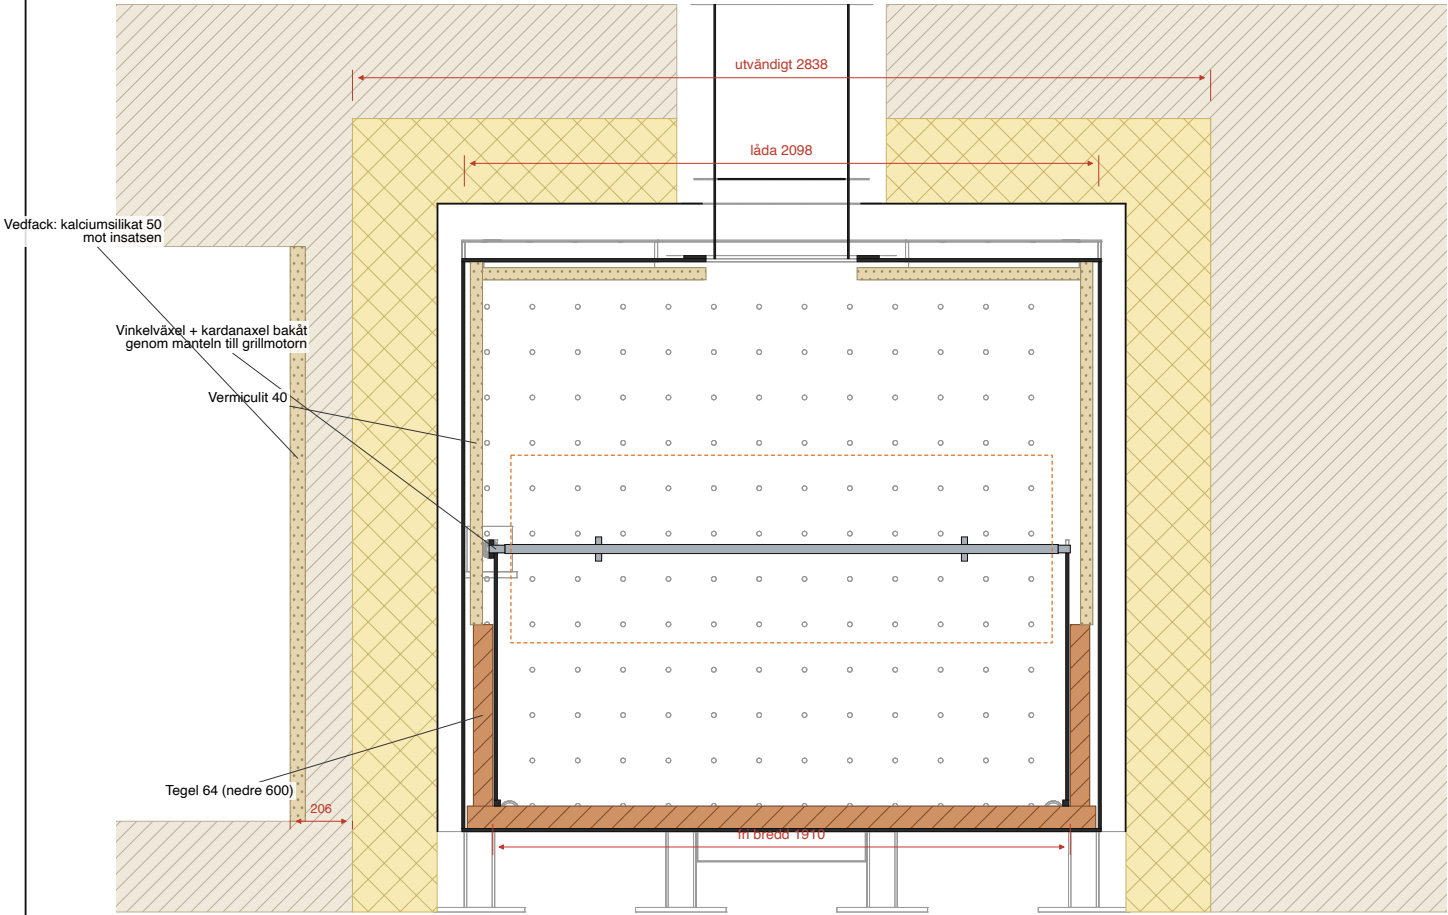

D–D genom takvingar och rökrör

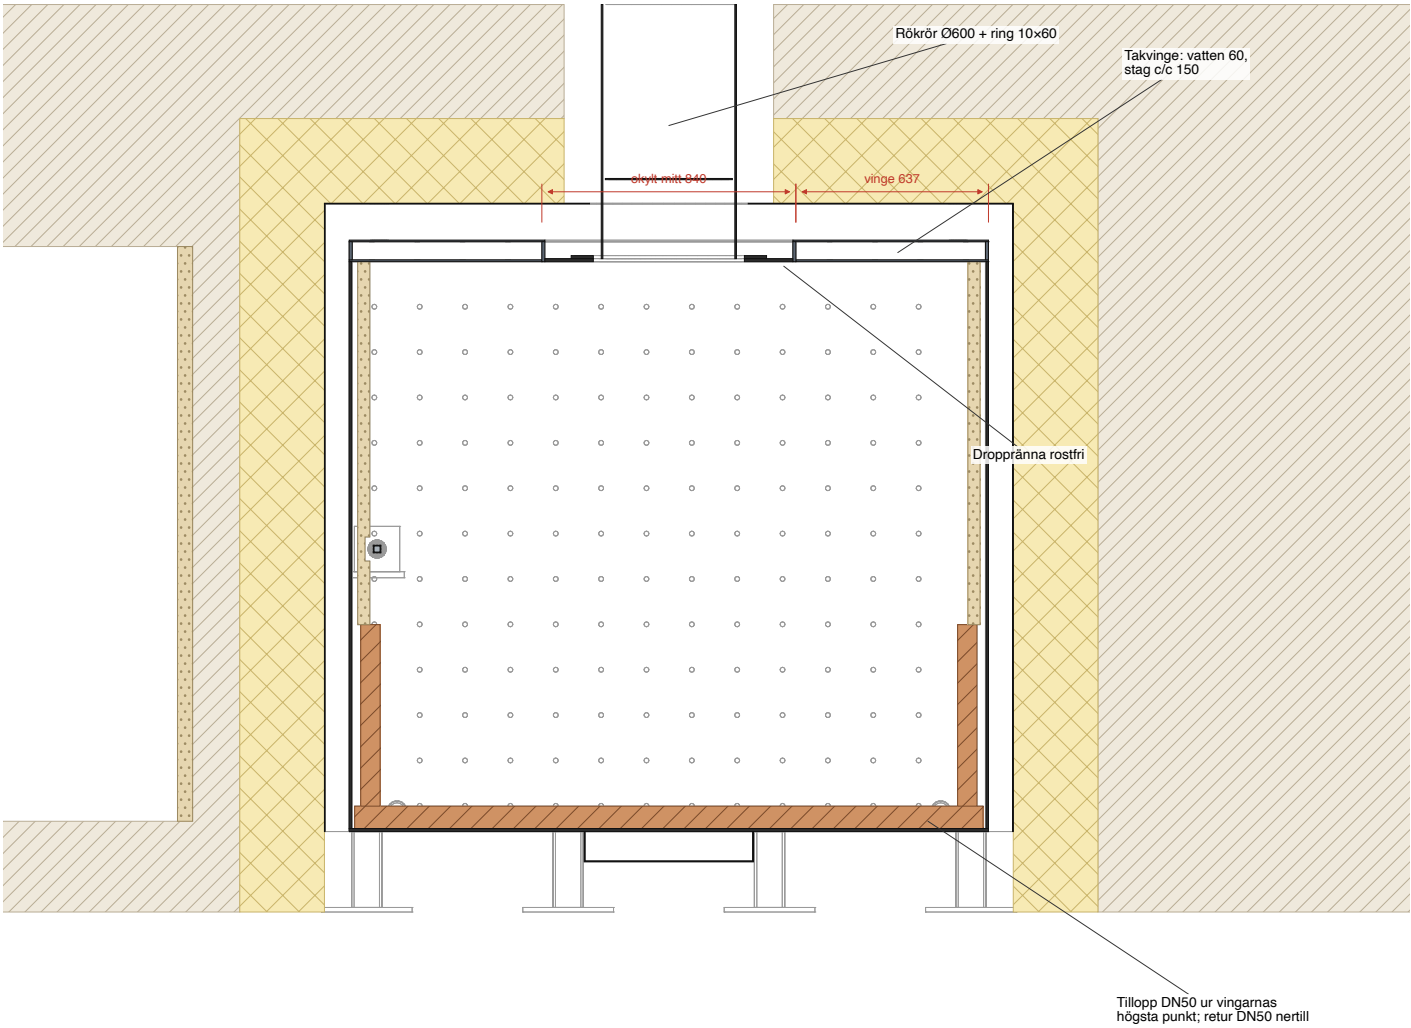

Snitt B–B och D–D · tvärs


B: genom spettet (y = 400) · D: genom takvingar och rökrör (y = 800)

Skala 1:25 (A3)


Garibaldi · Hugo Ljungberg · 2026-10-10 · mm

Blad 2 / 6


C–C plan i spetthöjd (z = 1200)

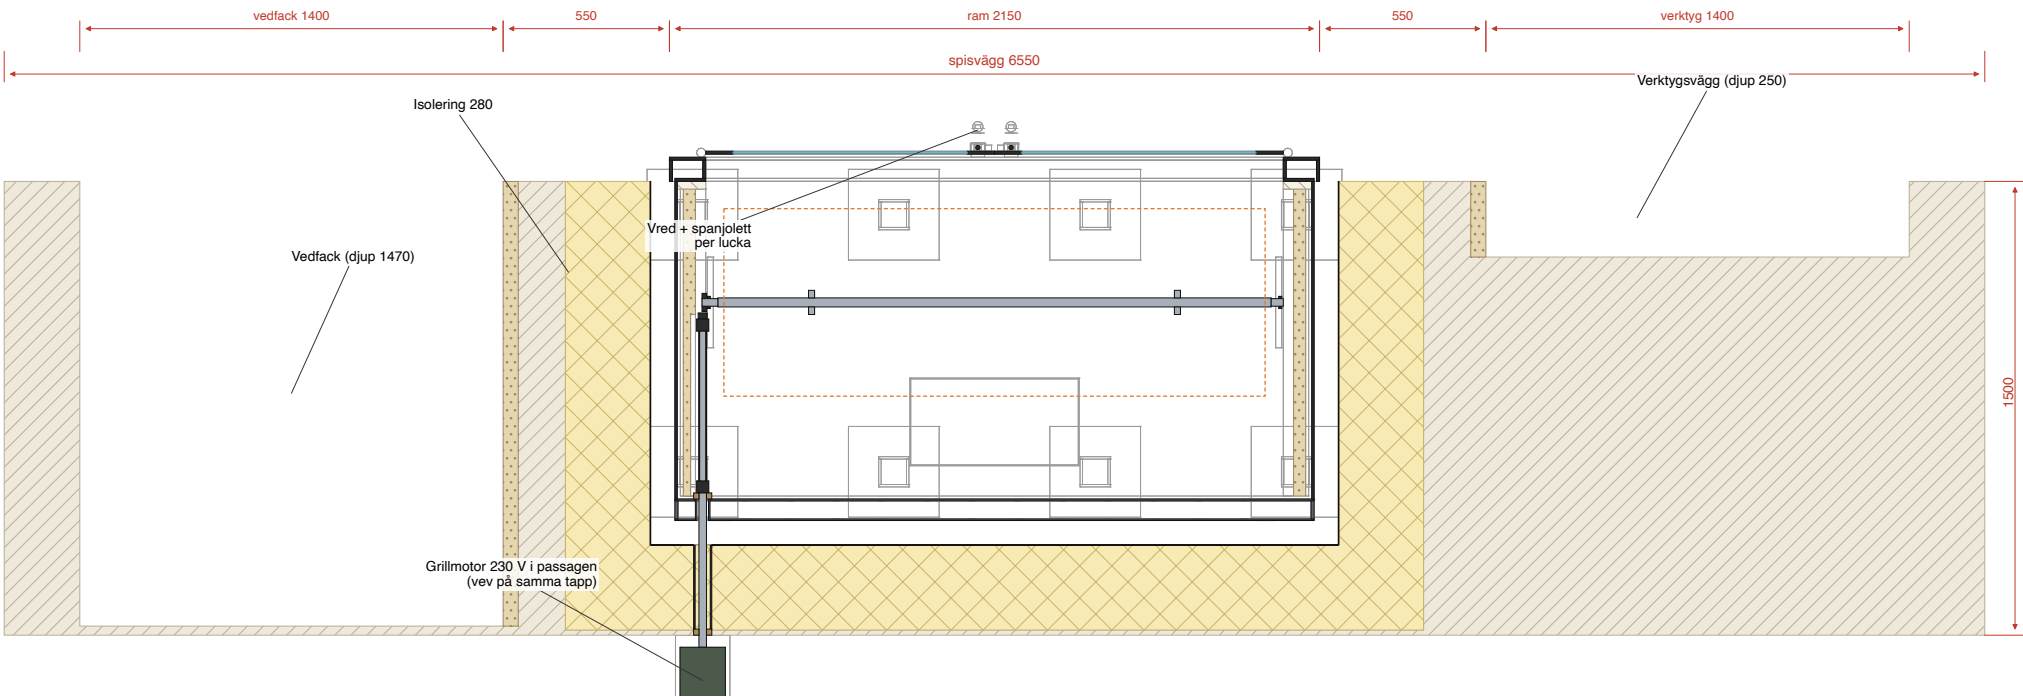

E–E plan genom takvingarnas vattenspalt (z = 2186)

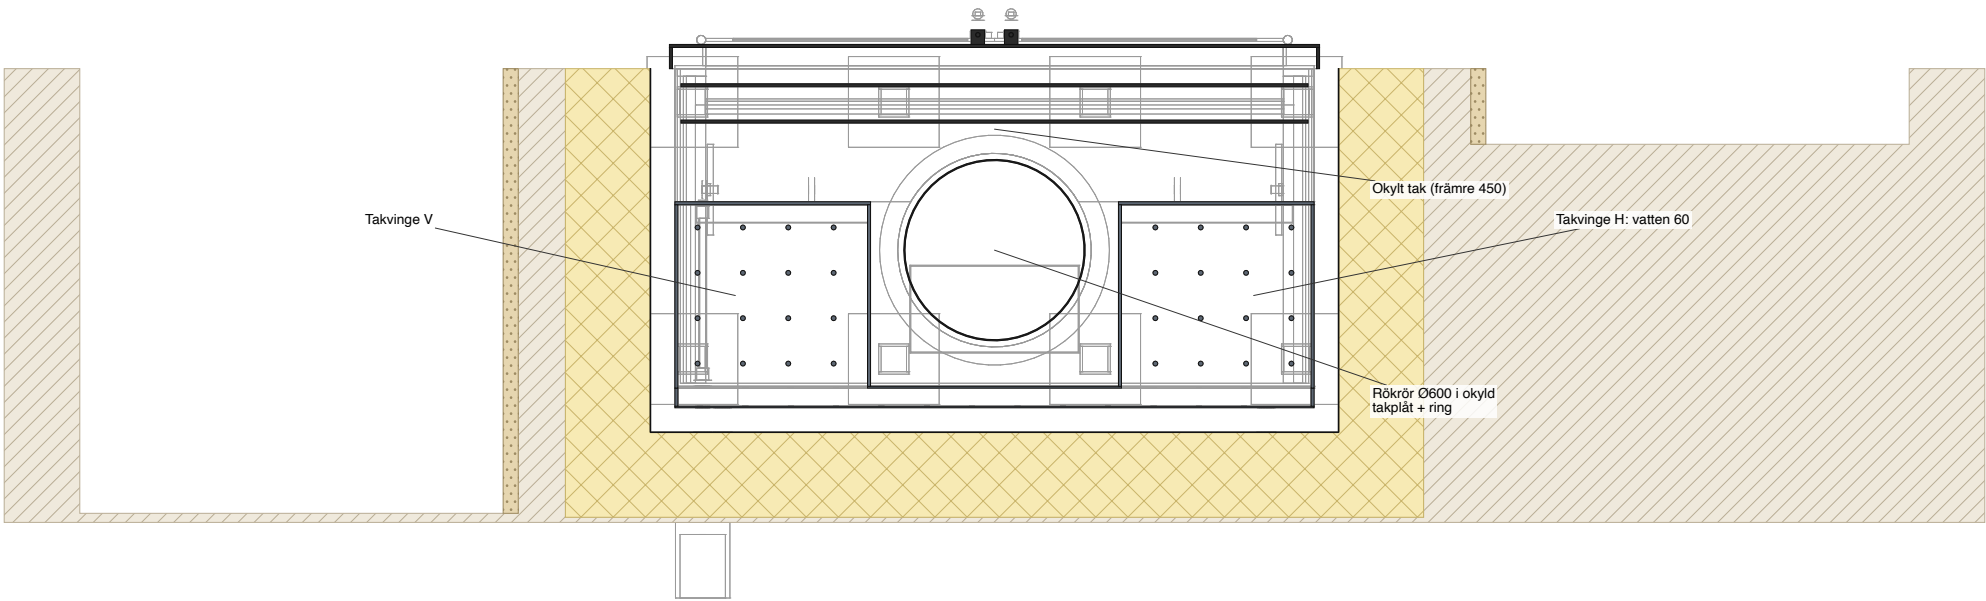

Snitt C–C och E–E · plan		
C: i spetthöjd (z = 1200) · E: genom takvingarnas vattenspalt (z = 2186)		Skala 1:25 (A3)
Garibaldi · Hugo Ljungberg · 2026-10-10 · mm		Blad 3 / 6

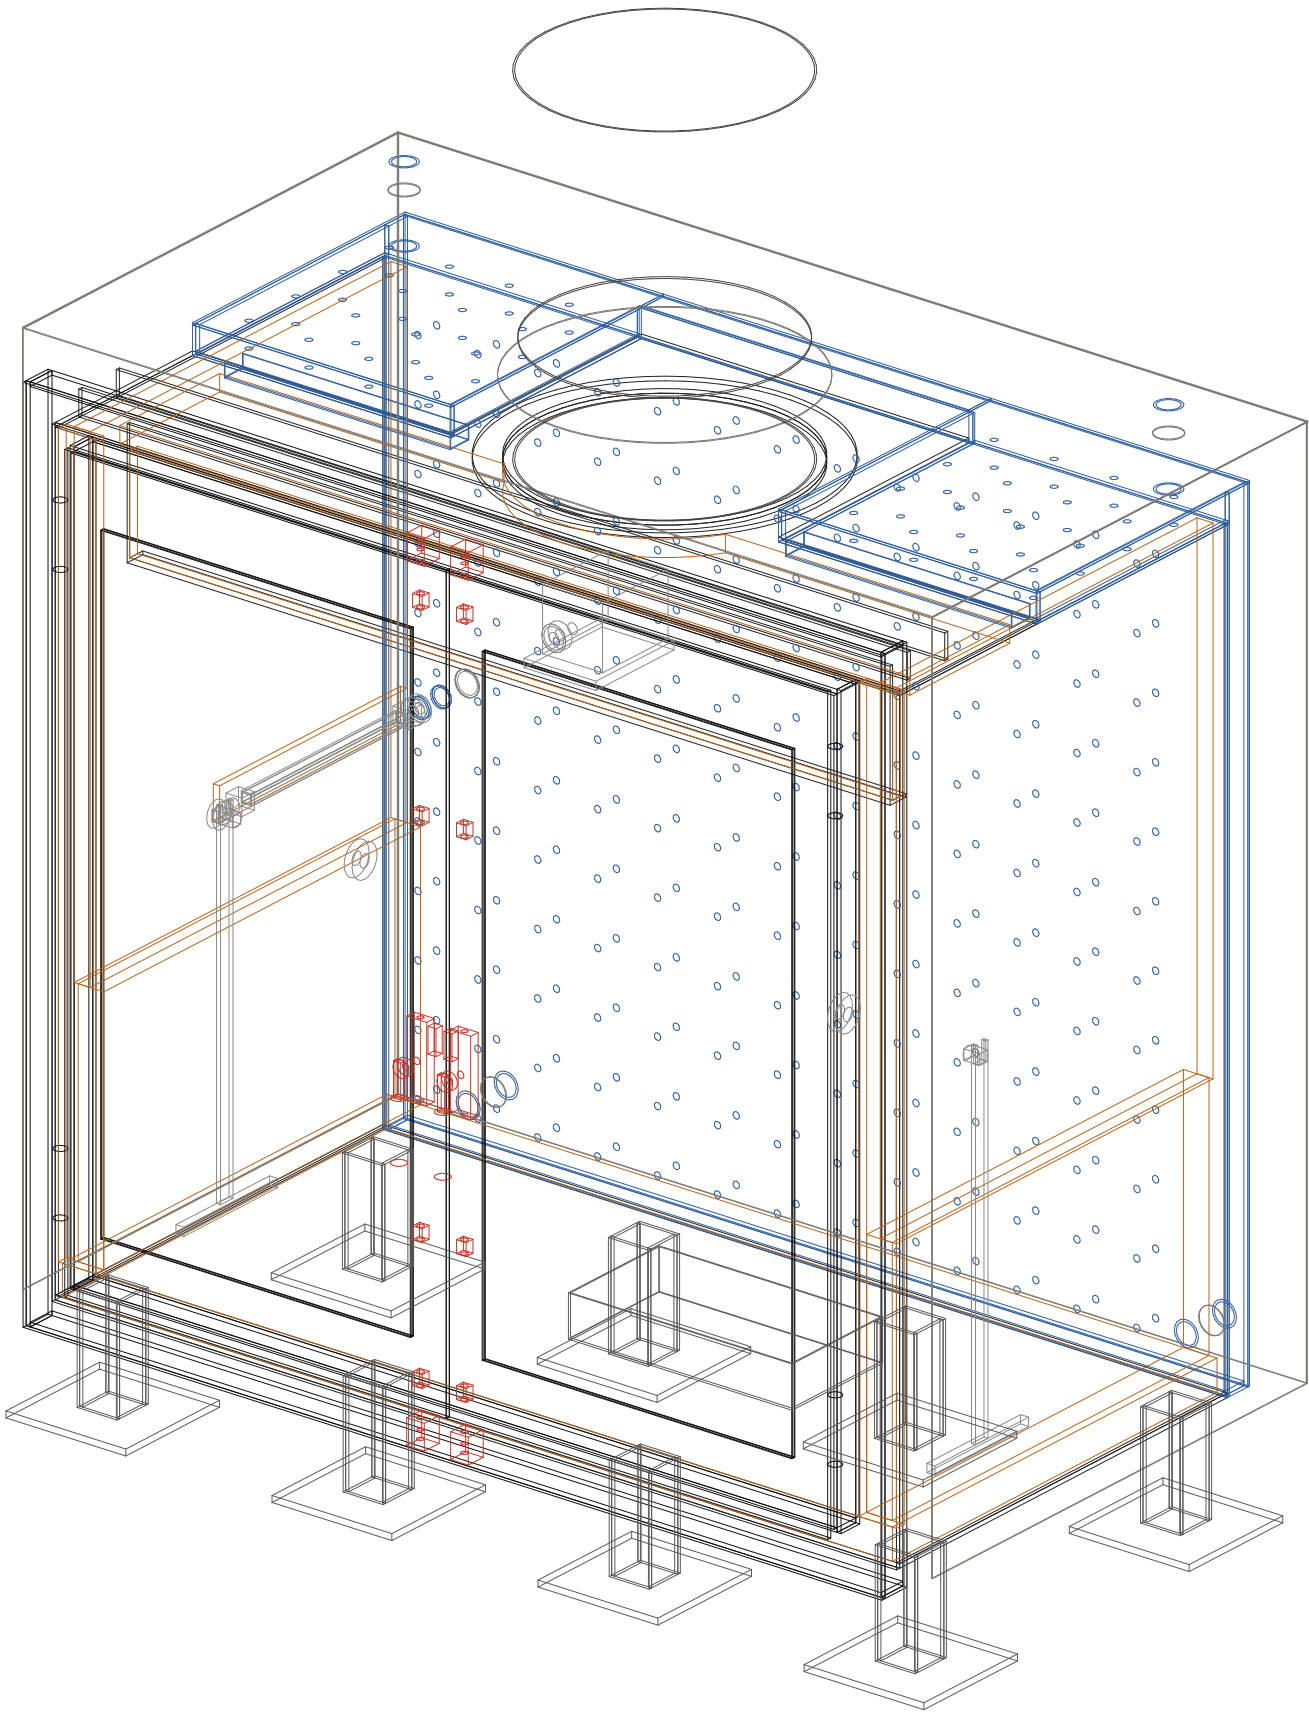

- Eldstadslåda
- Vattenmantel + stag
- Front och luckor
- Infodring
- Spett och drivning
- Konvektionsmantel
- Rökrör
- Ben och golv
- Lås och vred

Vikter ur modellen (kg)

Eldstadslåda	624
Vattenmantel + stag	496
Front och luckor	277
Infodring	550
Spett och drivning	42
Konvektionsmantel	190
Rökrör	58
Ben och golv	139
Lås och vred	15
Stål totalt	1840
Infodring	550
Vatten (ca 290 l)	290
I drift ≈ 2680 kg	



Axonometri · wireframe

Hela insatsen, färg per komponent (referenser dolda)

Skala ingen (A3)

Garibaldi · Hugo Ljungberg · 2026-10-10 · mm

Blad 4 / 6

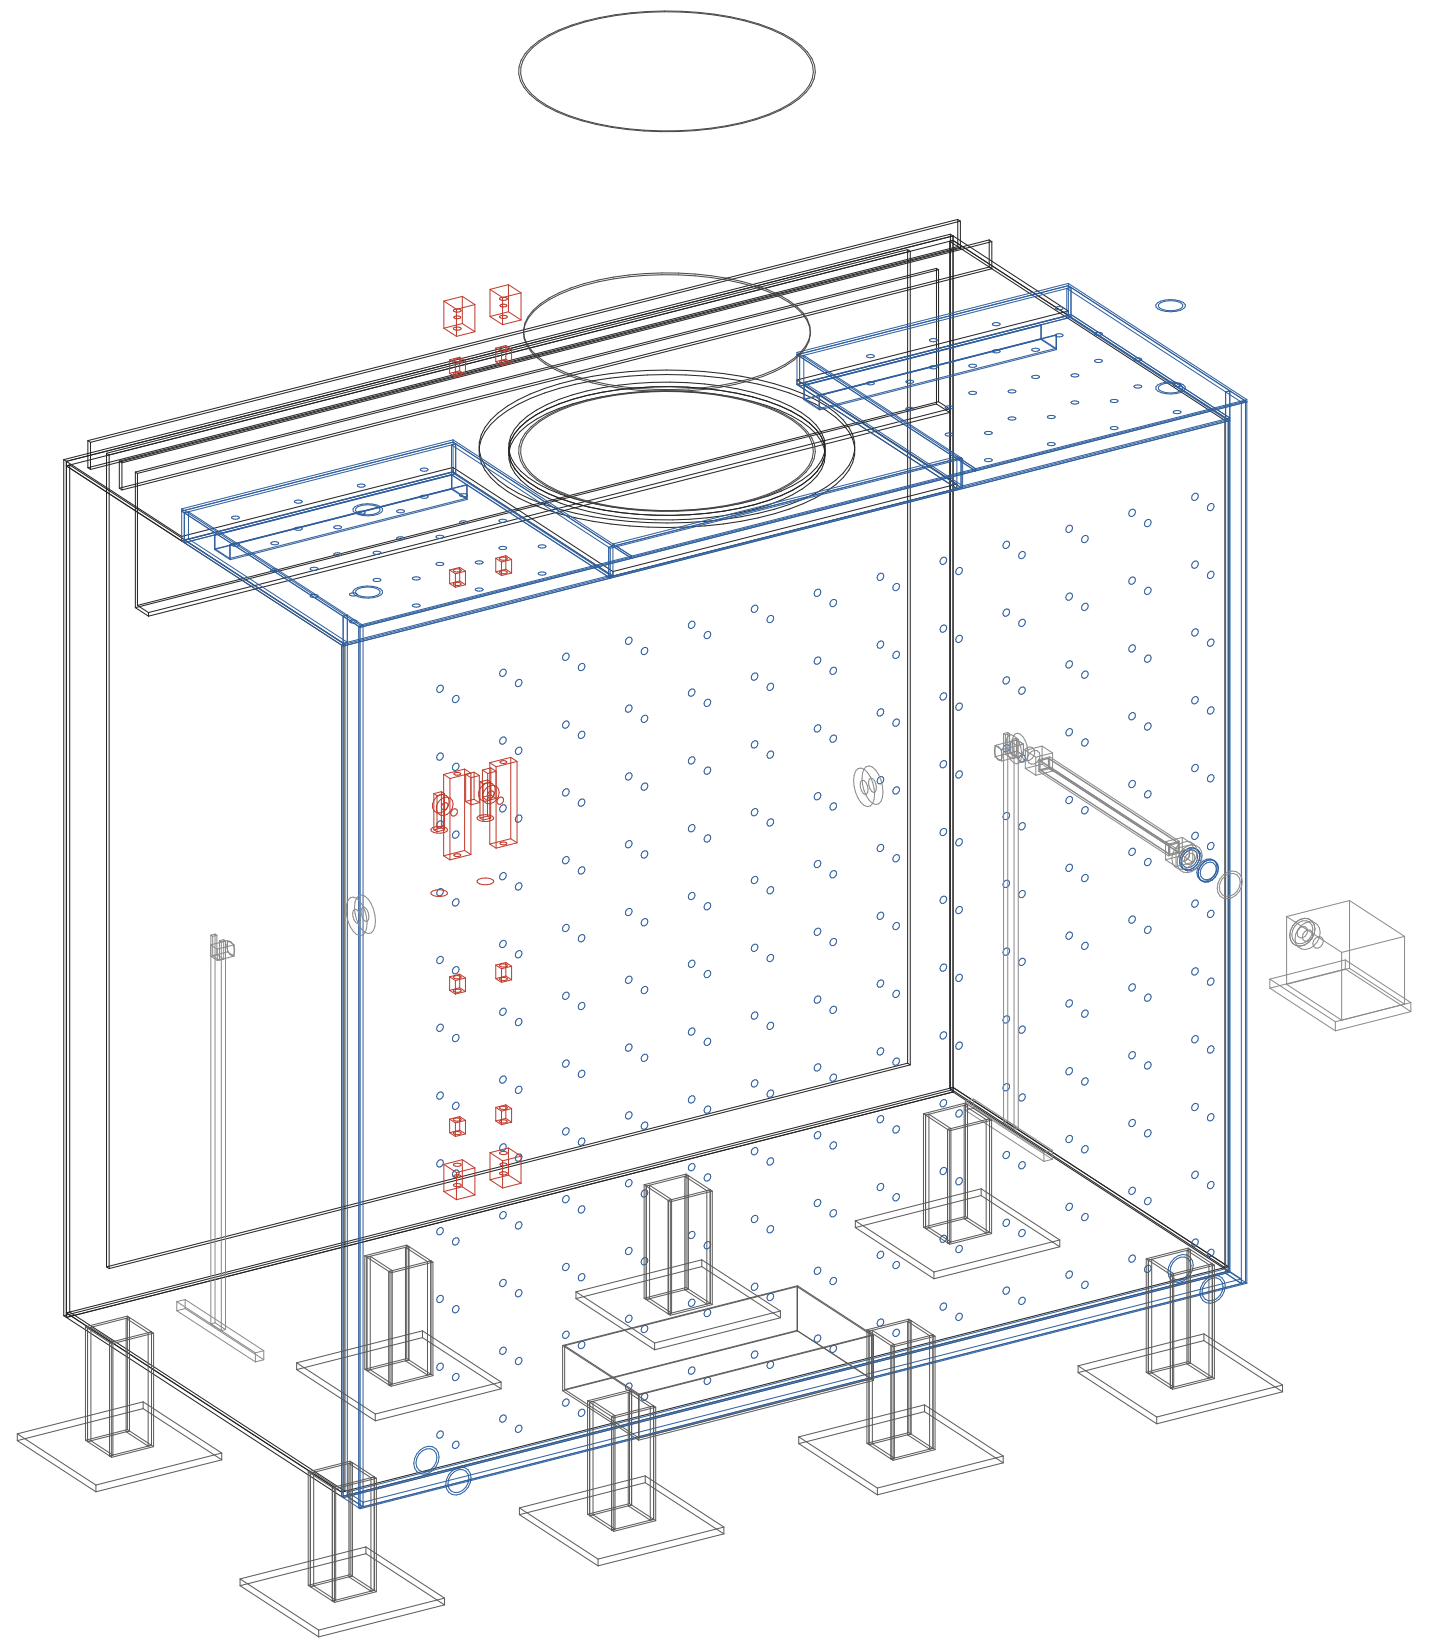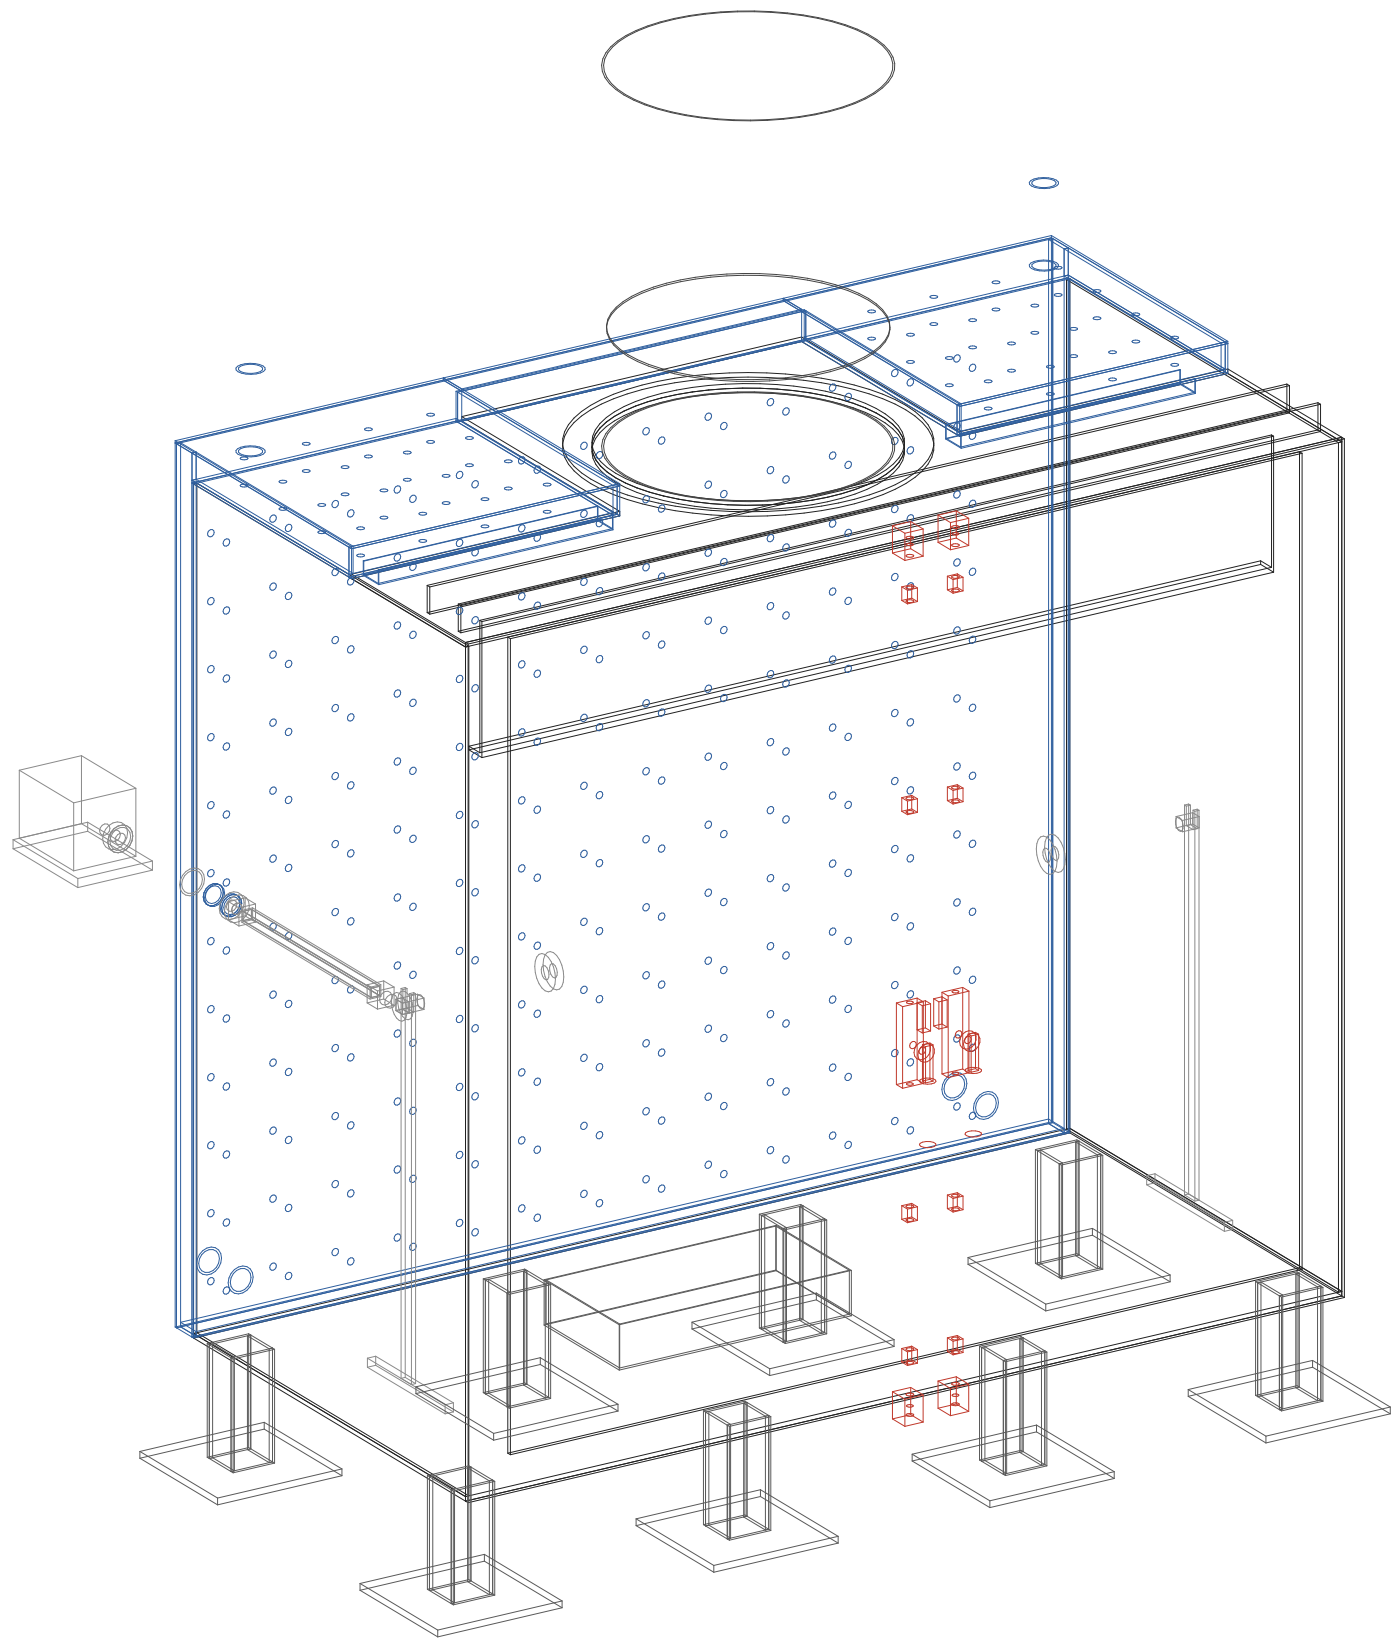

Axonometri · wireframe, inre delar

Vänster: utan front, konvektionsmantel och infodring · Höger: bakifrån (vattenmantel)

Skala ingen (A3)

Garibaldi · Hugo Ljungberg · 2026-10-10 · mm

Blad 5 / 6

OppB	1910 mm = 1910 mm · Eldstadsopppning bredd
OppH	1800 mm = 1800 mm · Eldstadsopppning hojd
Sill	350 mm = 350 mm · Oppningens underkant over salgolv
LadaD	1050 mm = 1050 mm · Eldstadsdjup, oppningsplan till bakmantel
TegelT	64 mm = 64 mm · Eldfast tegel
Bruk	10 mm = 10 mm · Eldfast bruk under golvtegel
InfSpalt	30 mm = 30 mm · Spalt tegel-stal sidor
TegelH	600 mm = 600 mm · Tegelzon pa sidorna
VermT	40 mm = 40 mm · Vermiculit
FiberT	25 mm = 25 mm · Keramisk fiber
LadaB	OppB + 2 * (TegelT + InfSpalt) = 2098 mm · Ladans innerbredd (fri bredd mellan tegel = OppB)
ZB	Sill – TegelT – Bruk = 276 mm · Stalbottnens ovansida
ZR	Sill + OppH = 2150 mm · Takets undersida
PlSida	8 mm = 8 mm · Sidovaggar
PlBotten	10 mm = 10 mm · Botten
PlTak	10 mm = 10 mm · Okyld takplat
XO	LadaB / 2 + PlSida = 1057 mm · Ladans yttre halvbredd
Mantellnre	6 mm = 6 mm · Mantelplat mot eld
MantelSpalt	60 mm = 60 mm · Vattenspalt
MantelYttre	5 mm = 5 mm · Yttre mantelplat
MantelKant	10 mm = 10 mm · Kantplattstang
VingeD	600 mm = 600 mm · Vattenkyld takzon baktill
RorD	600 mm = 600 mm · Rokror
RorFranBak	450 mm = 450 mm · Rokrorets centrum fran bakmantel
RingB	60 mm = 60 mm · Forstarkningsring bredd
VingeX0	RorD / 2 + 20 mm + RingB + 40 mm = 420 mm · Takvingarnas inre kant
StagCC	150 mm = 150 mm · Stag c/c

StagD	16 mm = 16 mm · Stag diameter
RamProfil	120 mm = 120 mm · Ramens bredd runt oppningen
RamT	10 mm = 10 mm · Ramplat
RamUt	80 mm = 80 mm · Ram framfor spisivaggen
LuckaT	10 mm = 10 mm · Luckplat
GlasKant	90 mm = 90 mm · Luckans ram runt glaset
HandtagZ	1100 mm = 1100 mm · Vredets hojd over salgolv
LasX	55 mm = 55 mm · Spanjolettstang fran mittfogen
LasStangD	14 mm = 14 mm · Spanjolettstang rundstal
LasIngrepp	35 mm = 35 mm · Stangens ingrepp i lasblecket (= slag vid 90 grader vred)
RokplatH	300 mm = 300 mm · Rokplat hojd
Rokplatin	100 mm = 100 mm · Rokplat innanfor front
RokplatT	8 mm = 8 mm · Rokplat tjocklek
RokplatKant	50 mm = 50 mm · Bockad kant
SpettY	400 mm = 400 mm · Spett fran front (300/400/500)
SpettZ	850 mm = 850 mm · Spett over eldstadsgolvet (650-1050)
SpettD	30 mm = 30 mm · Spett diameter
MotorD	210 mm = 210 mm · Grillmotorns djup bakom spisivaggen (i passagen)
HylsaD	48.3 mm = 48.3 mm · Genomforingsror genom vattenmanteln
KonvSpalt	80 mm = 80 mm · Konvektionsspalt sidor/bak
KonvSpaltTak	120 mm = 120 mm · Konvektionsspalt over tak
KonvT	2 mm = 2 mm · Konvektionsmantel
Iso	280 mm = 280 mm · Skikt 4-9 utanfor konvektionsmanteln
VaggT	1500 mm = 1500 mm · Spisvagg tjocklek
VaggB	6550 mm = 6550 mm · Spisvagg bredd
VaggH	3000 mm = 3000 mm · Spisvagg hojd
FackAvst	550 mm = 550 mm · Fack fran ramens kant

FackB	1400 mm = 1400 mm · Fackbredd
FackIso	50 mm = 50 mm · Kalciumsilikat fack-insats
BenFri	50 mm = 50 mm · Fri hojd under ladan (ben)

Parametrar (Fusion)	
Modify > Change Parameters · alla mått härleds härifrån	Skala – (A3)
Garibaldi · Hugo Ljungberg · 2026-10-10 · mm	Blad 6 / 6