
HALVBÅGE, SIDA (sett från husets insida) 1:15

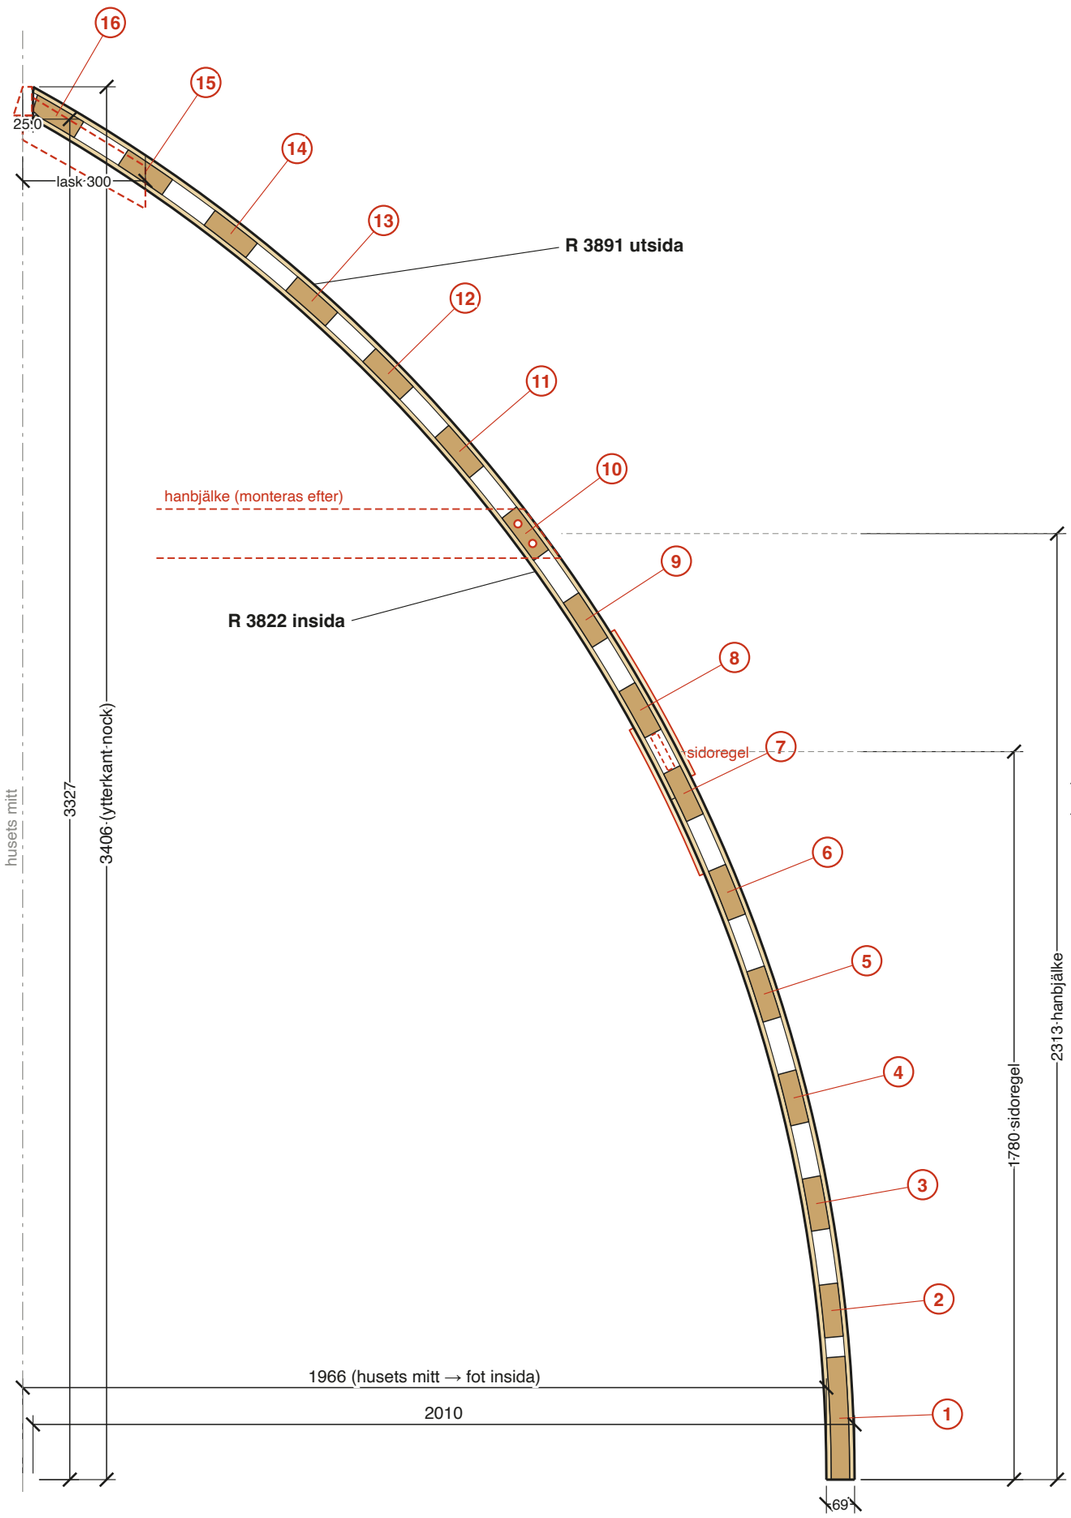


Cirkelns centrum: 1856 bortom husets mitt, i fotens nivå (andra halvans sida).

KLOSSAR – läge mätt längs YTTERKANTEN från foten (måttband på bågen)

nr	typ	längd	från	till	insida från	insida till
1	fot	300	0	303	0	297
2	kloss	130	352	483	346	475
3	kloss	130	619	750	608	737
4	kloss	130	885	1017	870	999
5	kloss	130	1152	1283	1132	1260
6	kloss	130	1419	1550	1393	1522
7	fack	130	1685	1816	1655	1784
8	fack	130	1917	2048	1883	2012
9	kloss	130	2177	2308	2139	2267
10	kloss (hanbj.)	130	2437	2568	2394	2523
11	kloss	130	2697	2828	2649	2778
12	kloss	130	2957	3088	2905	3034
13	kloss	130	3217	3348	3160	3289
14	kloss	130	3477	3608	3416	3544
15	kloss	130	3737	3868	3671	3800
16	nock	130	3998	4129	3927	4055


Fack för sidoregel 19×95 mellan fackklossarna = 100 fritt (2.5 spel/sida).
Ytterkant fot → nock ≈ 4148, insida ≈ 4036. Klossar c/c ≈ 264 nedre / 258 övre.
Nockklossens övre ände kapas lodrätt med flänsarna.

SNITT A-A (genom kloss) 1:2

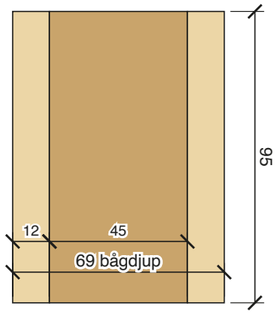

innerfläns 1 × 12 × 95 plywood
kloss regel 45×95 (45 radiellt, 95 tvärs bågen)
ytterfläns 1 × 12 × 95 plywood
flänsarna böjs runt klossarna: lim + 2 skruv 5×60 per fläns och kloss
skarv: en per fläns, mitt på en fackkloss + lask 400 (blad 3)

HEL BÅGE (2 halvor) 1:50

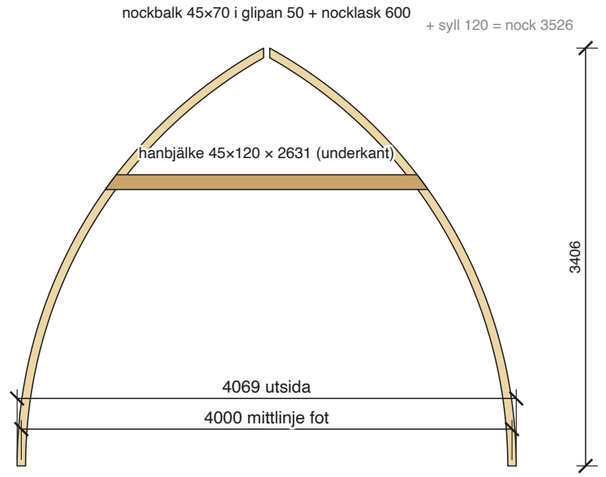

ANMÄRKNINGAR

Foten kapas vågrätt, nocken lodrätt. Flänsarna kapas med 25 mm övermått i ändarna och putsas efter montering.
Hanbjälke mitt på kloss 10: 2 bult M10×160, Ø11 genom klossen, ±30 från klossens mitt längs bågen.
Änden kapas snett längs bågen: överkant x = 1227, underkant x = 1316 från husets mitt.
Gavelbågar (4 halvor): ingen hanbjälke, nocklask bara på insidan.
Röd streckad = monteras senare (sidoregel, hanbjälke, nocklask). Röd heldragen = skarvlask.
Kontroll: två halvor ihop = 4000 c/c fot (mittlinjen), utsida 4069.

HALVBÅGE – FÄRDIG

18 st (2 per båge). Fläns 1 × 12 plywood, klossar regel 45×95.

Växthus buttercup · båge 1×12 · mått i mm · blad 1/3