
## HALVBÅGE, SIDA (sett från husets insida) 1:15

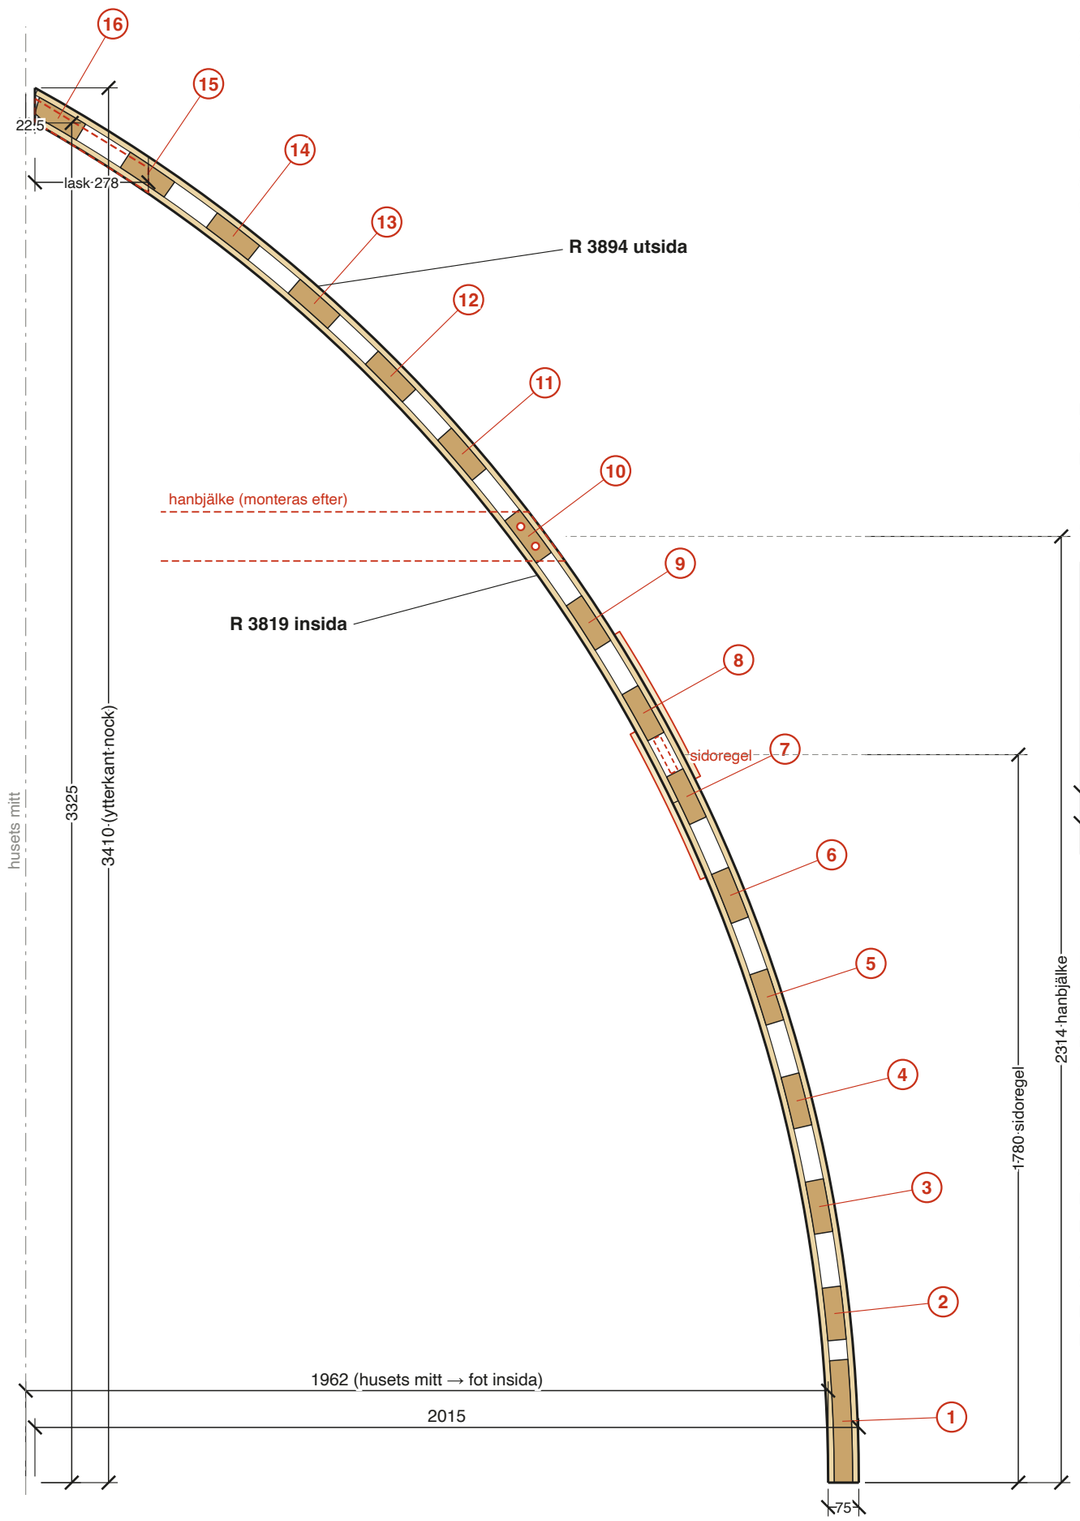



Cirkelns centrum: 1856 bortom husets mitt, i fotens nivå (andra halvans sida).

## KLOSSAR – läge mätt längs YTTERKANTEN från foten (måttband på bågen)

| nr | typ | längd | från | till | insida från | insida till |
|---|---|---|---|---|---|---|
| 1 | fot | 300 | 0 | 303 | 0 | 297 |
| 2 | kloss | 130 | 353 | 484 | 346 | 475 |
| 3 | kloss | 130 | 619 | 751 | 607 | 736 |
| 4 | kloss | 130 | 886 | 1017 | 869 | 998 |
| 5 | kloss | 130 | 1153 | 1284 | 1131 | 1259 |
| 6 | kloss | 130 | 1420 | 1551 | 1392 | 1521 |
| 7 | fack | 130 | 1686 | 1818 | 1654 | 1783 |
| 8 | fack | 130 | 1919 | 2050 | 1882 | 2010 |
| 9 | kloss | 130 | 2179 | 2311 | 2137 | 2266 |
| 10 | kloss (hanbj.) | 130 | 2440 | 2571 | 2393 | 2522 |
| 11 | kloss | 130 | 2701 | 2832 | 2648 | 2777 |
| 12 | kloss | 130 | 2961 | 3092 | 2904 | 3033 |
| 13 | kloss | 130 | 3222 | 3353 | 3160 | 3288 |
| 14 | kloss | 130 | 3482 | 3614 | 3415 | 3544 |
| 15 | kloss | 130 | 3743 | 3874 | 3671 | 3800 |
| 16 | nock | 130 | 4004 | 4135 | 3926 | 4055 |


Fack för sidoregel 19×95 mellan fackklossarna = 100 fritt (2.5 spel/sida).
Ytterkant fot → nock ≈ 4156, insida ≈ 4034. Klossar c/c ≈ 264 nedre / 258 övre.
Nockklossens övre ände kapas lodrätt med flänsarna.

## SNITT A-A (genom kloss) 1:2

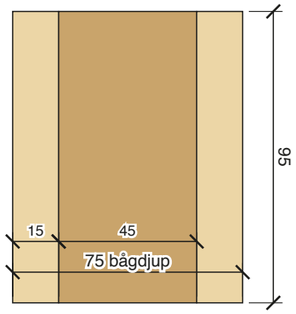


innerfläns 1 × 15 × 95 plywood
kloss regel 45×95 (45 radiellt, 95 tvärs bågen)
ytterfläns 1 × 15 × 95 plywood
flänsarna böjs runt klossarna: lim + 2 skruv 5×60 per fläns och kloss
skarv: en per fläns, mitt på en fackkloss + lask 400 (blad 3)

## HEL BÅGE (2 halvor) 1:50

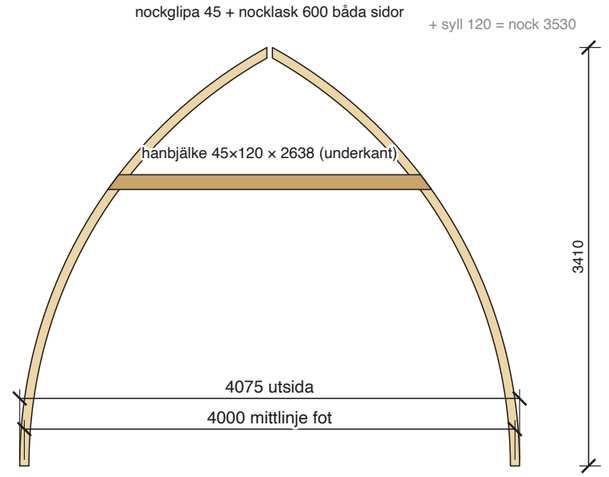


## ANMÄRKNINGAR

Foten kapas vågrätt, nocken lodrätt. Flänsarna kapas med 25 mm övermått i ändarna och putsas efter montering.
Hanbjälke mitt på kloss 10: 2 bult M10×160, Ø11 genom klossen, ±30 från klossens mitt längs bågen.
Änden kapas snett längs bågen: överkant x = 1230, underkant x = 1319 från husets mitt.
Gavelbågar (4 halvor): ingen hanbjälke, nocklask bara på insidan.
Röd streckad = monteras senare (sidoregel, hanbjälke, nocklask). Röd heldragen = skarvlask.
Kontroll: två halvor ihop = 4000 c/c fot (mittlinjen), utsida 4075.

## HALVBÅGE – FÄRDIG

18 st (2 per båge). Fläns 1 × 15 plywood, klossar regel 45×95.

Växthus buttercup · båge 1×15 · mått i mm · blad 1/3