
HALVBÅGE, SIDA (sett från husets insida, +y) 1:15

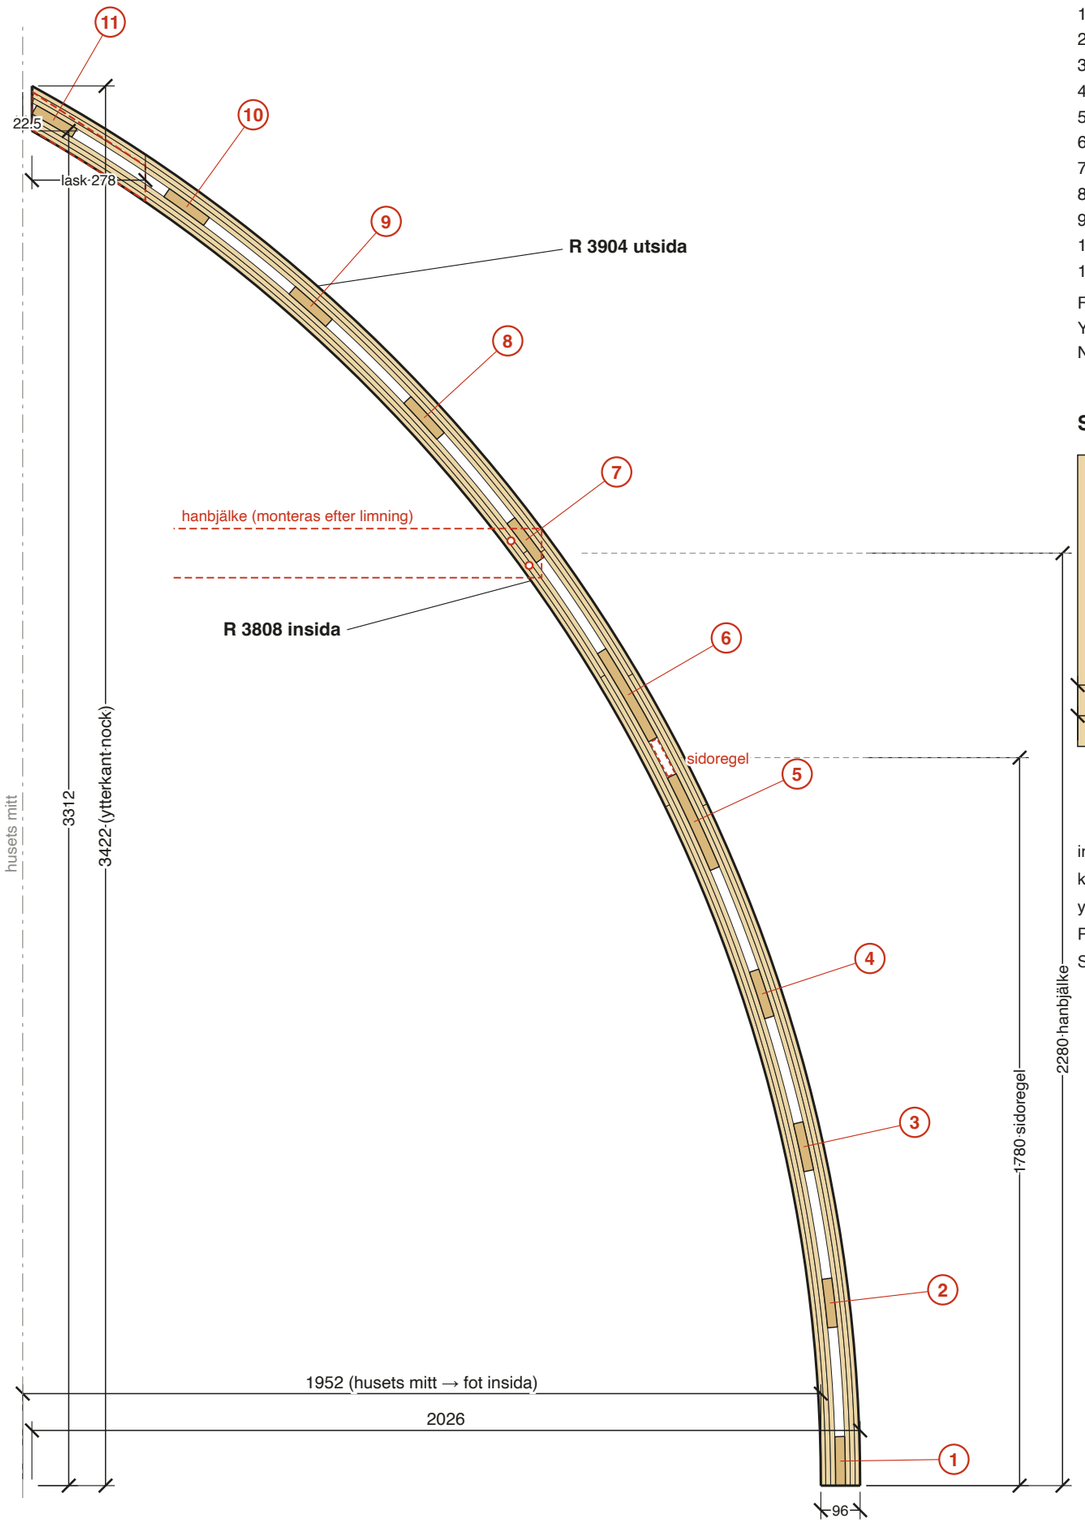


Cirkelns centrum: 1856 bortom husets mitt, i fotens nivå (andra halvans sida).

KLOSSAR – läge mätt längs YTTERKANTEN från foten (måttband på bågen)

nr	typ	längd	från	till	insida från	insida till
1	fot	120	0	121	0	119
2	kloss	120	392	514	383	501
3	kloss	120	785	906	765	884
4	kloss	120	1177	1299	1148	1267
5	fack	250	1569	1823	1531	1778
6	fack	250	1924	2177	1877	2123
7	kloss	120	2449	2571	2389	2508
8	kloss	120	2843	2965	2773	2892
9	kloss	120	3237	3358	3157	3276
10	kloss	120	3631	3752	3541	3660
11	nock	120	4024	4146	3925	4044


Fack för sidoregel 19×95 mellan kloss 4 och 5 = 100 fritt (2.5 spel/sida).
Ytterkantens totala längd fot → nock ≈ 4173, insidans ≈ 4017.
Nockklossens övre ände kapas lodrätt med flänsarna (29° mot radien).

SNITT A-A (genom kloss) 1:2

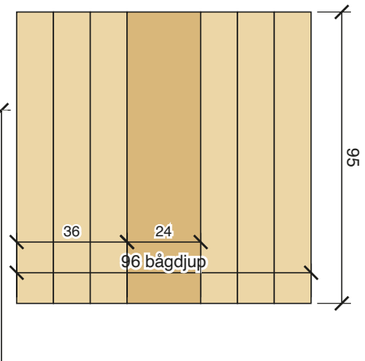

innerfläns 3 × 12 plywood (lager 1–3, 1 innerst)
kloss 2 × 12 plywood, limmad + 2 skruv 5×90 utifrån
ytterfläns 3 × 12 plywood (lager 4–6, 6 ytterst)
PU-lim i alla fogar, pressas med kilar i mallen
Skarvar: se blad 2 (lager i olika lägen, ≈ 364 isär)

HEL BÅGE (2 halvor) 1:50

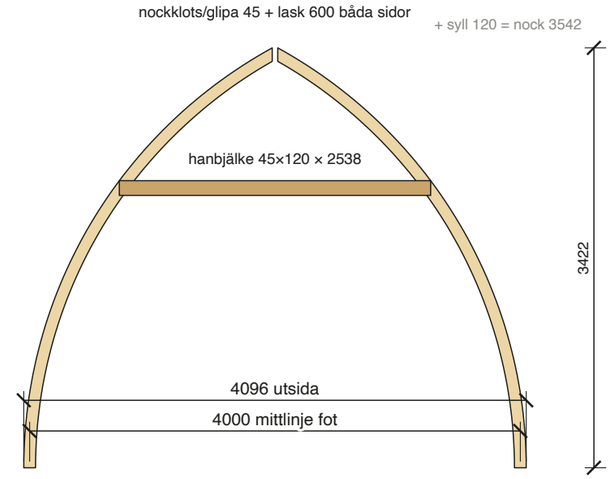

ANMÄRKNINGAR

Foten kapas vågrätt (= radiellt), nocken lodrätt. Flänsarna limmas med 25 mm övermått i båda ändar.
Hanbjälke: 2 bulthål Ø11 genom innerflänsen på 2250 och 2310 över foten,
x = 1238 och 1194 från husets mitt. Hanbjälkens ände kapas lodrätt i x = 1269.
Gavelbågar (4 halvor): ingen hanbjälke, nocklask bara på insidan.
Röd streckad = delar som monteras senare (sidoregel, hanbjälke, nocklask).
Kontroll: två halvor ihop = 4000 c/c fot (mittlinjen), utsida 4096.

HALVBÅGE – FÄRDIG

18 st (2 per båge). Limmas en och en i mallen.

Växthus buttercup · båge B · mått i mm · blad 1/3