
HALVBÅGE, SIDA (sett från husets insida) 1:15

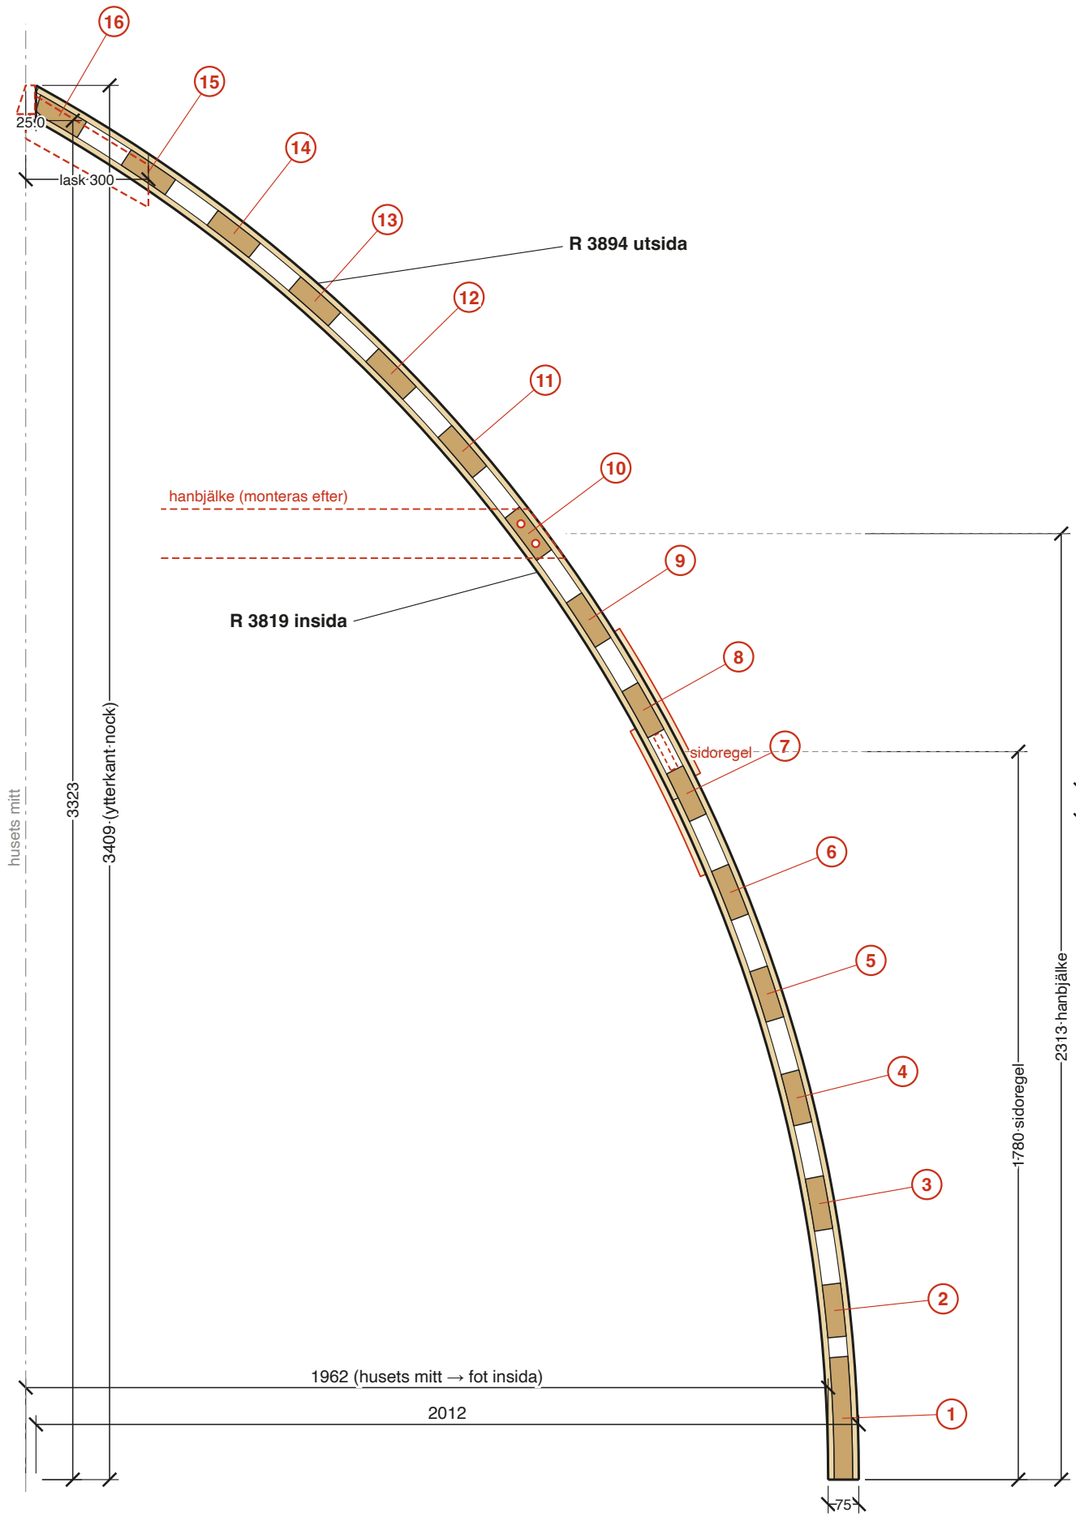


Cirkelns centrum: 1856 bortom husets mitt, i fotens nivå (andra halvans sida).

KLOSSAR – läge mätt längs YTTERKANTEN från foten (måttband på bågen)

nr	typ	längd	från	till	insida från	insida till
1	fot	300	0	303	0	297
2	kloss	130	353	484	346	475
3	kloss	130	619	751	607	736
4	kloss	130	886	1017	869	998
5	kloss	130	1153	1284	1131	1259
6	kloss	130	1420	1551	1392	1521
7	fack	130	1686	1818	1654	1783
8	fack	130	1919	2050	1882	2010
9	kloss	130	2179	2310	2137	2266
10	kloss (hanbj.)	130	2439	2570	2392	2521
11	kloss	130	2699	2831	2647	2776
12	kloss	130	2960	3091	2902	3031
13	kloss	130	3220	3351	3158	3286
14	kloss	130	3480	3611	3413	3542
15	kloss	130	3740	3871	3668	3797
16	nock	130	4001	4132	3924	4052


Fack för sidoregel 19×95 mellan fackklossarna = 100 fritt (2.5 spel/sida).
Ytterkant fot → nock ≈ 4153, insida ≈ 4031. Klossar c/c ≈ 264 nedre / 258 övre.
Nockklossens övre ände kapas lodrätt med flänsarna.

SNITT A-A (genom kloss) 1:2

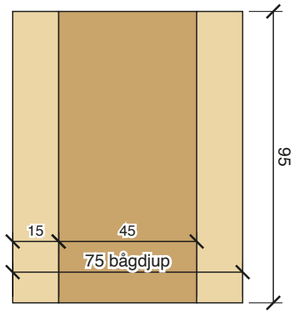

innerfläns 1 × 15 × 95 plywood
kloss regel 45×95 (45 radiellt, 95 tvärs bågen)
ytterfläns 1 × 15 × 95 plywood
flänsarna böjs runt klossarna: lim + 2 skruv 5×60 per fläns och kloss
skarv: en per fläns, mitt på en fackkloss + lask 400 (blad 3)

HEL BÅGE (2 halvor) 1:50

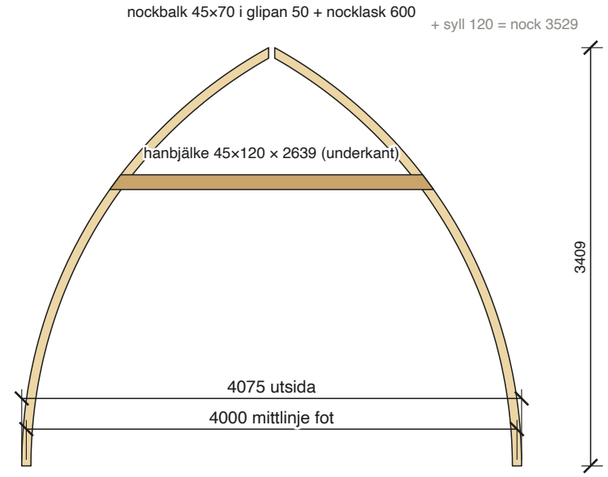

ANMÄRKNINGAR

Foten kapas vågrätt, nocken lodrätt. Flänsarna kapas med 25 mm övermått i ändarna och putsas efter montering.
Hanbjälke mitt på kloss 10: 2 bult M10×160, Ø11 genom klossen, ±30 från klossens mitt längs bågen.
Änden kapas snett längs bågen: överkant x = 1231, underkant x = 1319 från husets mitt.
Gavelbågar (4 halvor): ingen hanbjälke, nocklask bara på insidan.
Röd streckad = monteras senare (sidoregel, hanbjälke, nocklask). Röd heldragen = skarvlask.
Kontroll: två halvor ihop = 4000 c/c fot (mittlinjen), utsida 4075.

HALVBÅGE – FÄRDIG

18 st (2 per båge). Fläns 1 × 15 plywood, klossar regel 45×95.


REMSOR 95 × 15 ur konstruktionsplywood 15 × 2500 × 1200 (raka snitt, sågsnitt 3)

KAPPLISTA – EN HALVBÅGE (4 flänsbitar + 2 skarvlaskar). Flänsbitar med 25 mm övermått i ytteränden.

fläns	radie (mitt)	båglängd	skarv vid	bit A (fot)	bit B (nock)
inner	R 3826	4043	1722	**1747**	**2347**
ytter	R 3886	4141	1980	**2005**	**2185**
lask				**2 × 400**	(en per skarv)


Skarven mäts längs flänsens egen kant från foten och ligger mitt på en fackkloss (innerfläns nedre, ytterfläns övre).
Bitarna läggs stumt med lim i ändarna; lasken limmas och skruvas över skarven.
Totalt 18 halvbågar: 72 flänsbitar (en remsa var) + 36 laskar (6 per remsa)
= 78 remsor = 7 skivor (12 remsor per skiva). Spillet från bit B räcker ofta till laskarna.

SKARVLÄGEN, utvikt (fot till vänster, nock till höger) ca 1:24

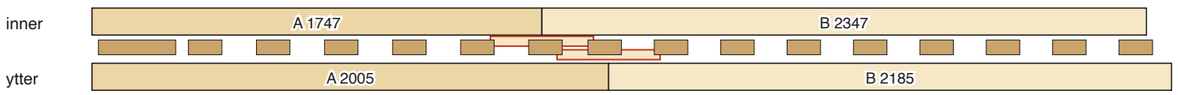


brunt mellan flänsarna = klossarnas lägen, röd = skarvlask

SKIVPLAN – 1 skiva 2500 × 1200 → 12 remsor 1:14

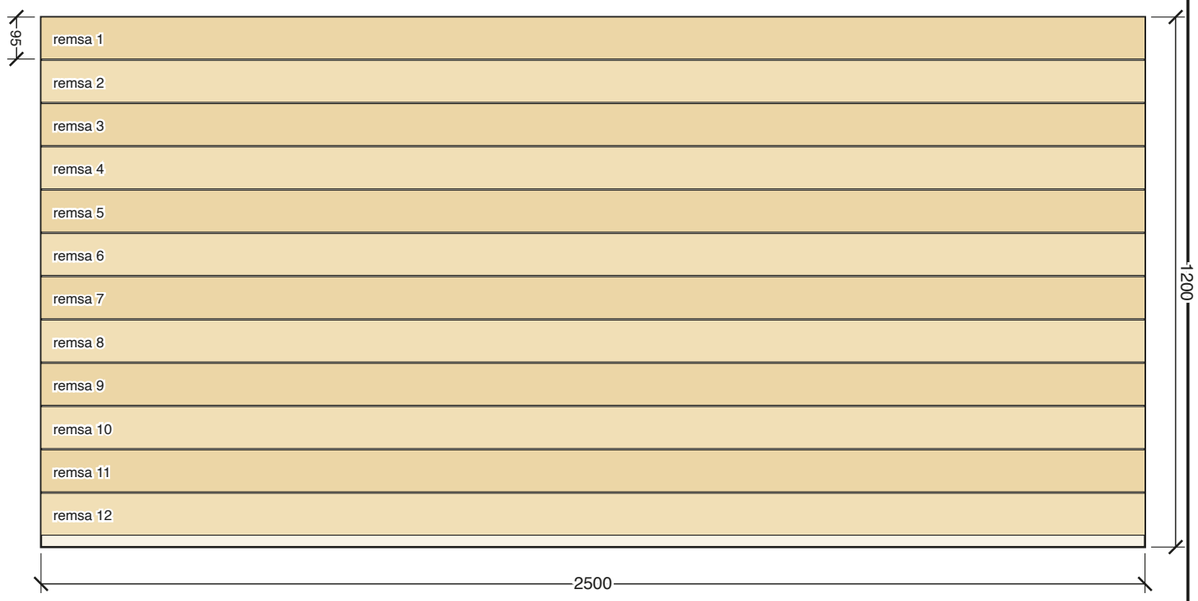

12 × 95 + 11 snitt × 3 = 1173; rest 27 mm.
Såga längs skivans långa riktning (ytskiktets fibrer längs remsan).
Anslagslist + cirkelsåg / spårsåg; samma anslag till alla remsor.

EN REMSA: flänsbit + spill

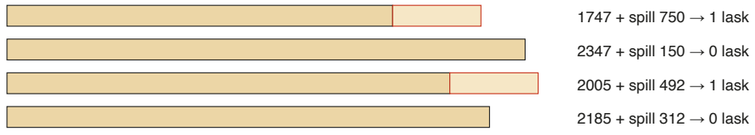


PLYWOODREMSOR

Kapplista per halvbåge + skivplan

Växthus buttercup · båge 1×15 · mått i mm · blad 2/3

KLOSSAR AV REGEL 45×95 1:2

Kloss 130 (vanlig, fack och nock)

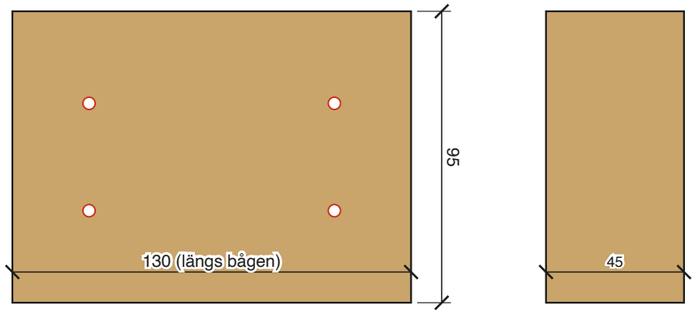


regel 45×95, kapas

15 per halvbåge = 270 st

röda = skruv 5×60 genom flänsen

(2 från insidan, 2 från utsidan)

Fotkloss 300

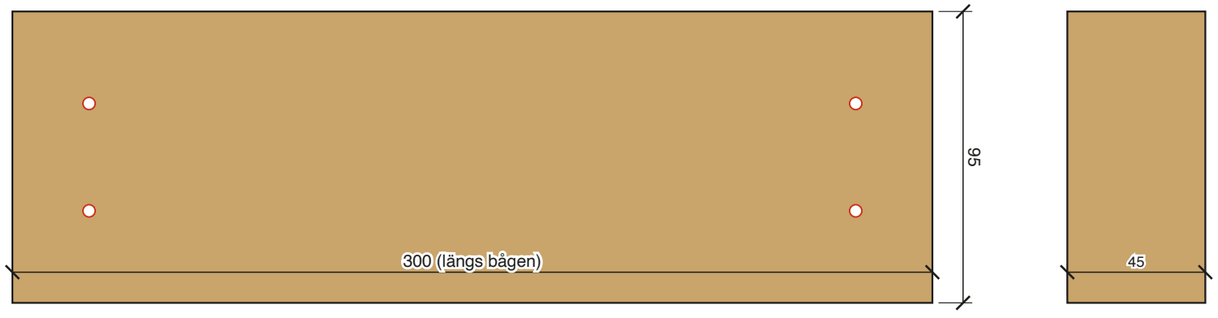

regel 45×95, kapas

1 per halvbåge = 18 st

röda = skruv 5×60 genom flänsen


(2 från insidan, 2 från utsidan)

Regel 45×95 totalt ≈ 41 m (+ spill). Kapa vinkelrätt, alla klossar lika.

Klossen är rak och flänsen böjd: på 130 blir glipan mot innerflänsen under 1 mm, på fotklossen ca 3 mm – limmet fyller.

Nockklossen läggs med övermått och kapas lodrätt tillsammans med flänsarna.

SKARVLASK 15 × 95 × 400 plywood 1:4

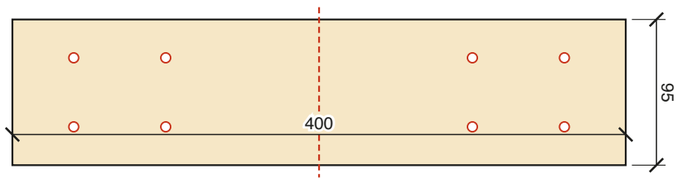


Ytterfläns: lasken på utsidan. Innerfläns: på insidan.

Skarven (röd streckad) mitt på lasken = mitt på fackklossen.

PU-lim + 8 skruv 4,5×25. 36 st totalt.

NOCKLASK 15 mm plywood 1:4

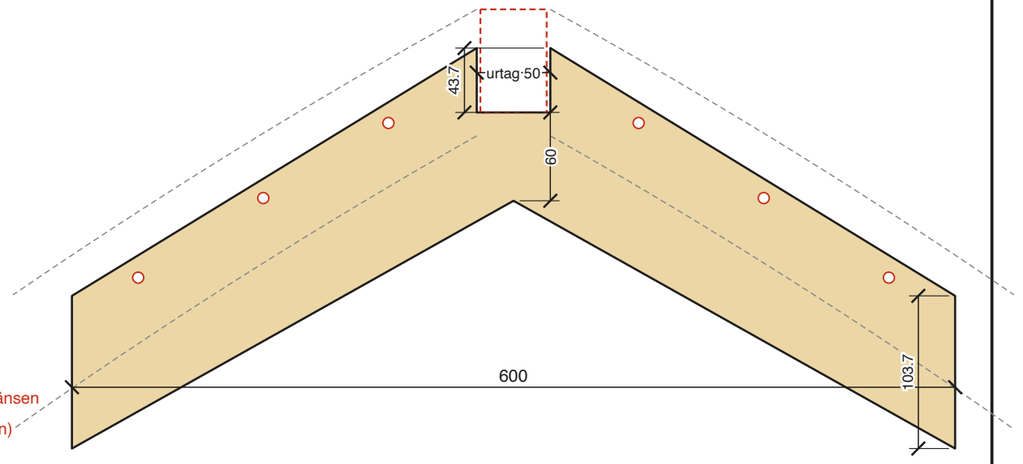

Hörn (x från mitten, ned = mm under ytterkanten i nocken):

A ände, överkant	x = ±300.0	**ned 194.6**
B urtagets kant, överkant	x = ±25.0	**ned 26.3**
C urtagets botten	x = ±25.0	**ned 70.0**
D ände, underkant	x = ±300.0	**ned 298.3**
E mitt, underkant	x = ±0.0	**ned 130.0**

Raka snitt. Urtaget (50 × 44) är där nockbalken 45×70 vilar.

Överkanten 23 under bågens ytterkant så att nockens låsprofil går fri.

Röda = skruv 4,5×40 i flänsar och nockkloss + PU-lim. Gör en mall av den första.

Antal: 2 per inre båge + 1 per gavelbåge (insidan) = 16 st.

KLOSSAR OCH LASKAR

Raka snitt. Klossar av regel 45×95.

Växthus buttercup · båge 1×15 · mått i mm · blad 3/3