
HALVBÅGE, SIDA (sett från husets insida) 1:15

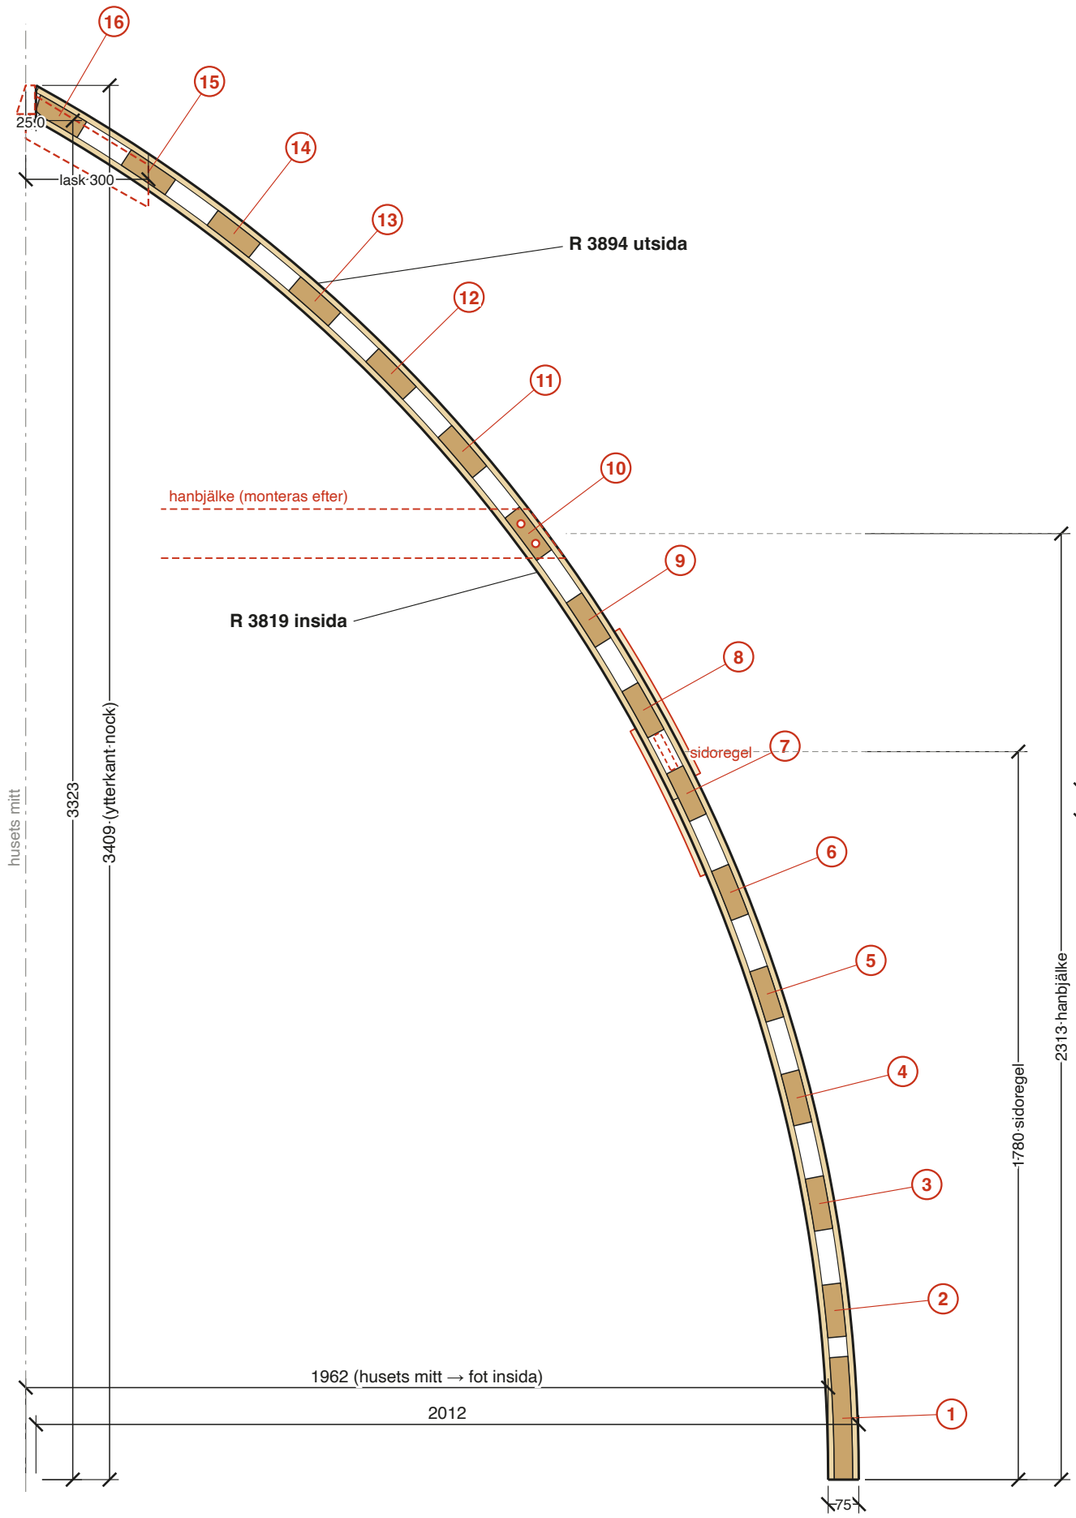


Cirkelns centrum: 1856 bortom husets mitt, i fotens nivå (andra halvans sida).

KLOSSAR – läge mätt längs YTTERKANTEN från foten (måttband på bågen)

nr	typ	längd	från	till	insida från	insida till
1	fot	300	0	303	0	297
2	kloss	130	353	484	346	475
3	kloss	130	619	751	607	736
4	kloss	130	886	1017	869	998
5	kloss	130	1153	1284	1131	1259
6	kloss	130	1420	1551	1392	1521
7	fack	130	1686	1818	1654	1783
8	fack	130	1919	2050	1882	2010
9	kloss	130	2179	2310	2137	2266
10	kloss (hanbj.)	130	2439	2570	2392	2521
11	kloss	130	2699	2831	2647	2776
12	kloss	130	2960	3091	2902	3031
13	kloss	130	3220	3351	3158	3286
14	kloss	130	3480	3611	3413	3542
15	kloss	130	3740	3871	3668	3797
16	nock	130	4001	4132	3924	4052


Fack för sidoregel 19×95 mellan fackklossarna = 100 fritt (2.5 spel/sida).
Ytterkant fot → nock ≈ 4153, insida ≈ 4031. Klossar c/c ≈ 264 nedre / 258 övre.
Nockklossens övre ände kapas lodrätt med flänsarna.

SNITT A-A (genom kloss) 1:2

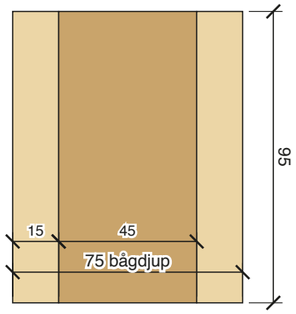

innerfläns 1 × 15 × 95 plywood
kloss regel 45×95 (45 radiellt, 95 tvärs bågen)
ytterfläns 1 × 15 × 95 plywood
flänsarna böjs runt klossarna: lim + 2 skruv 5×60 per fläns och kloss
skarv: en per fläns, mitt på en fackkloss + lask 400 (blad 3)

HEL BÅGE (2 halvor) 1:50

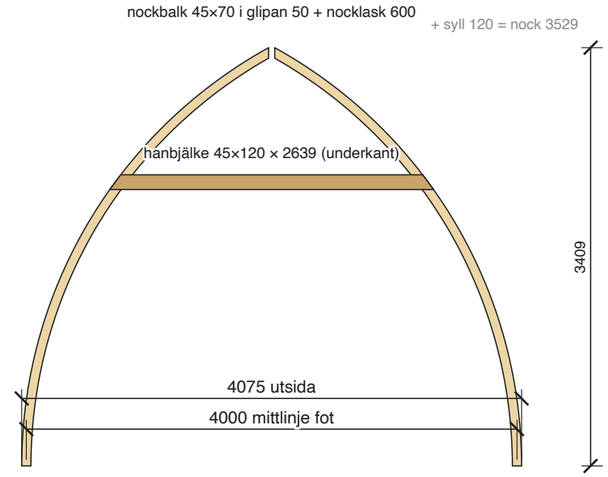

ANMÄRKNINGAR

Foten kapas vågrätt, nocken lodrätt. Flänsarna kapas med 25 mm övermått i ändarna och putsas efter montering.
Hanbjälke mitt på kloss 10: 2 bult M10×160, Ø11 genom klossen, ±30 från klossens mitt längs bågen.
Änden kapas snett längs bågen: överkant x = 1231, underkant x = 1319 från husets mitt.
Gavelbågar (4 halvor): ingen hanbjälke, nocklask bara på insidan.
Röd streckad = monteras senare (sidoregel, hanbjälke, nocklask). Röd heldragen = skarvlask.
Kontroll: två halvor ihop = 4000 c/c fot (mittlinjen), utsida 4075.

HALVBÅGE – FÄRDIG

18 st (2 per båge). Fläns 1 × 15 plywood, klossar regel 45×95.