



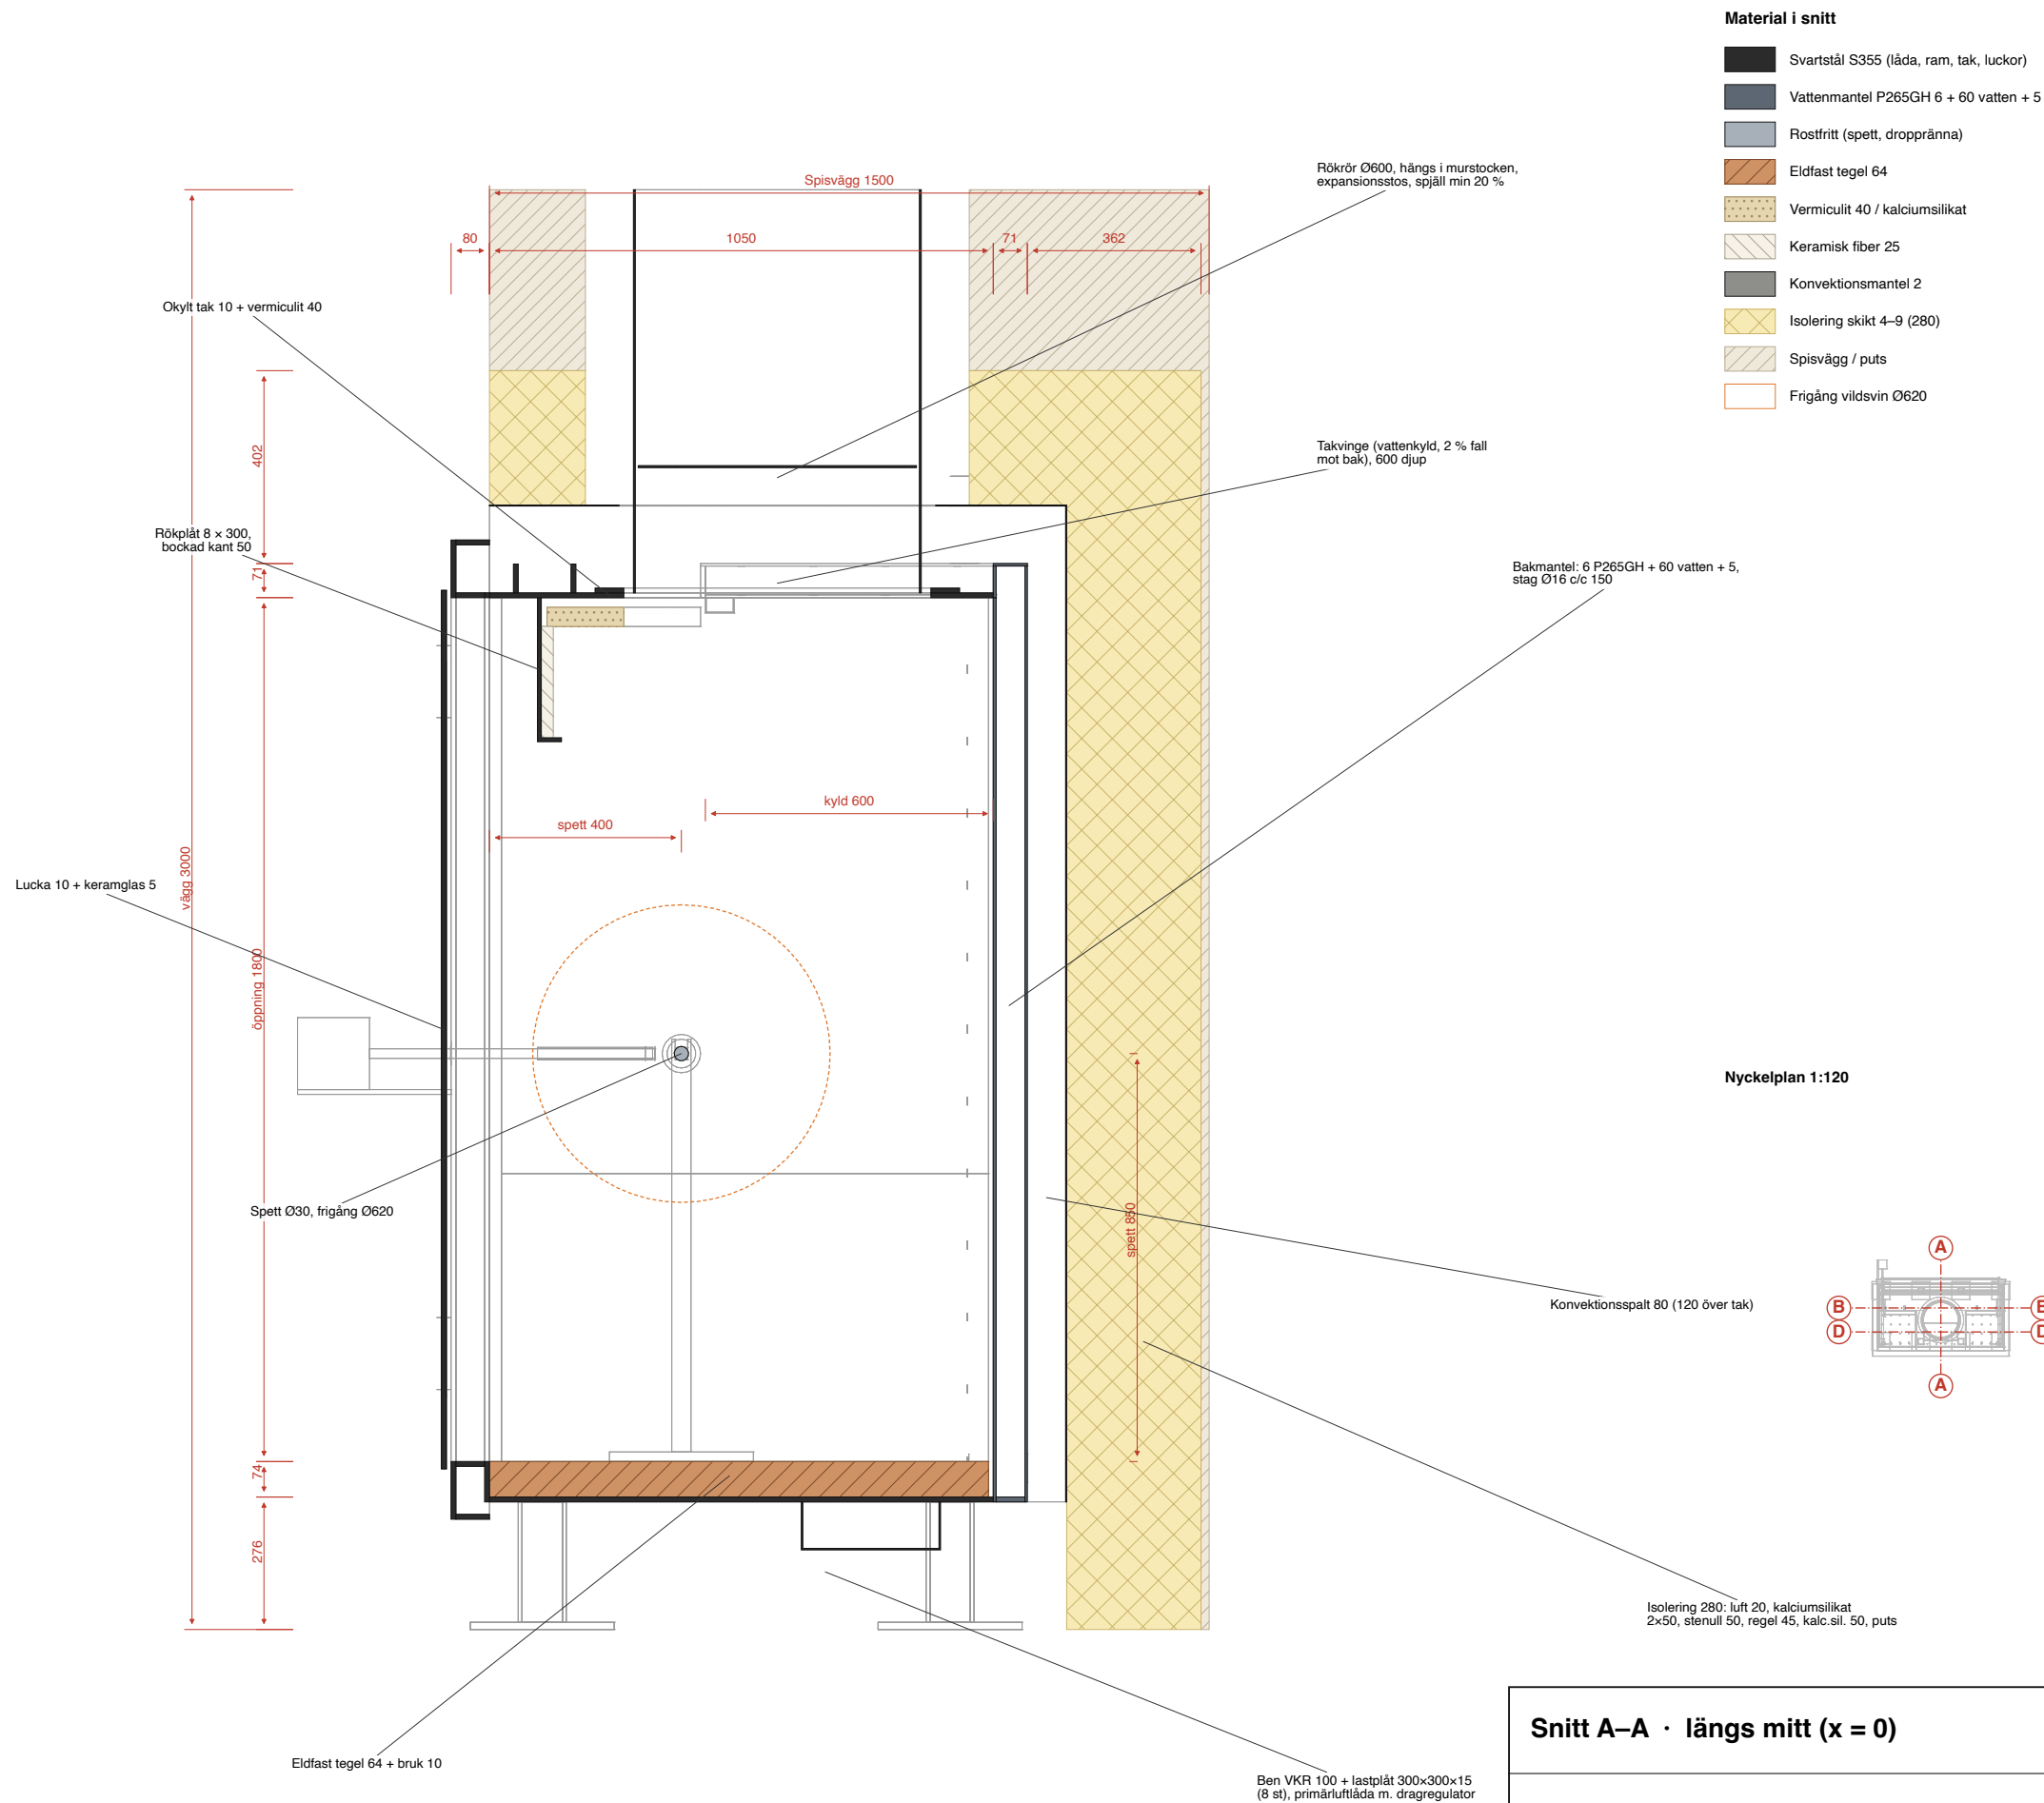


Snitt A–A · längs mitt (x = 0)		
Eldstadsinsats v3 · vattenmantlad bakvägg + takvingar		Skala 1:15 (A3)
Garibaldi · Hugo Ljungberg · 2026-10-10 · mm		Blad 1 / 6

- Svartstål S355 (låda, ram, tak, luckor)
- Vattenmantel P265GH 6 + 60 vatten + 5
- Rostfritt (spett, droppränna)
- Eldfast tegel 64
- Vermiculit 40 / kalciumsilikat
- Keramisk fiber 25
- Konvektionsmantel 2
- Isolering skikt 4–9 (280)
- Spisvägg / puts
- Frigång vildsvin Ø620

B–B genom spettet

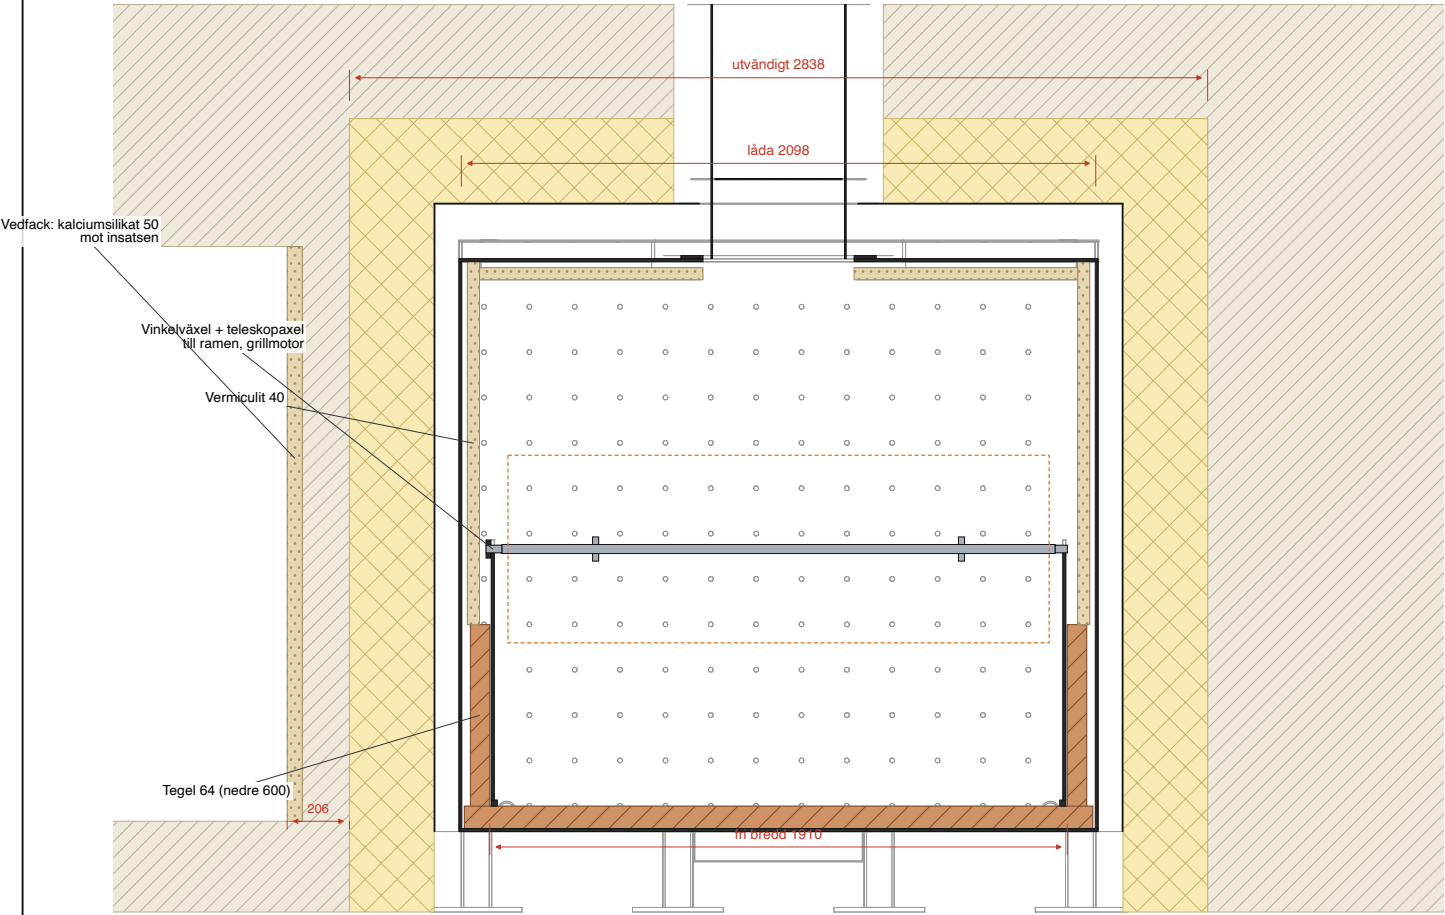

D–D genom takvingar och rökrör

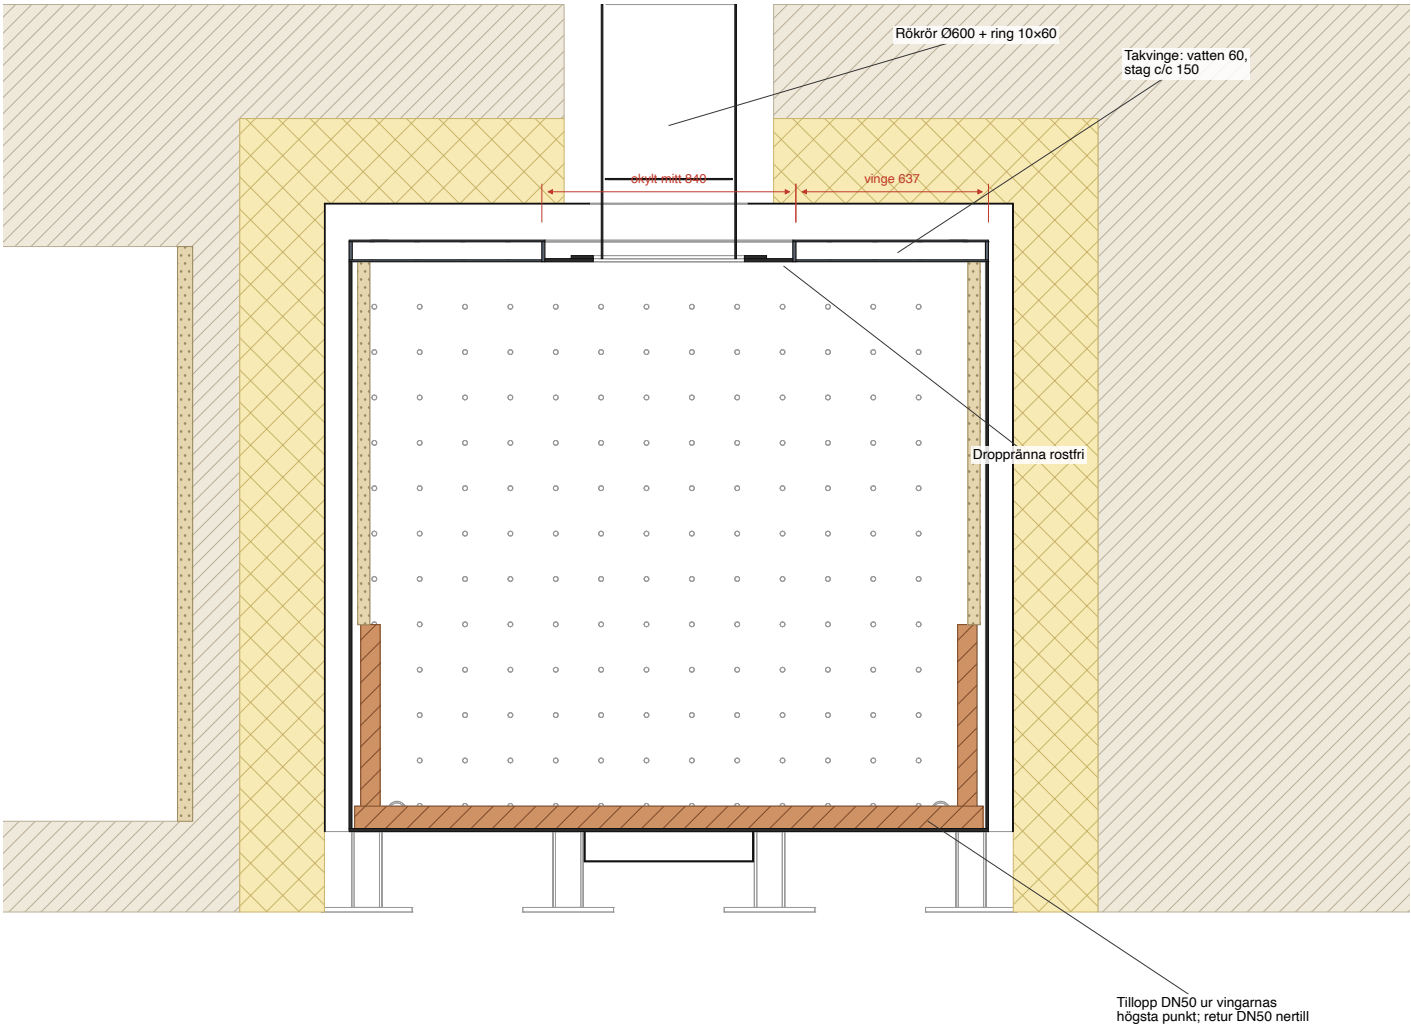

Snitt B–B och D–D · tvärs


B: genom spettet (y = 400) · D: genom takvingar och rökrör (y = 800)

Skala 1:25 (A3)


Garibaldi · Hugo Ljungberg · 2026-10-10 · mm

Blad 2 / 6

C–C plan i spetthöjd (z = 1200)

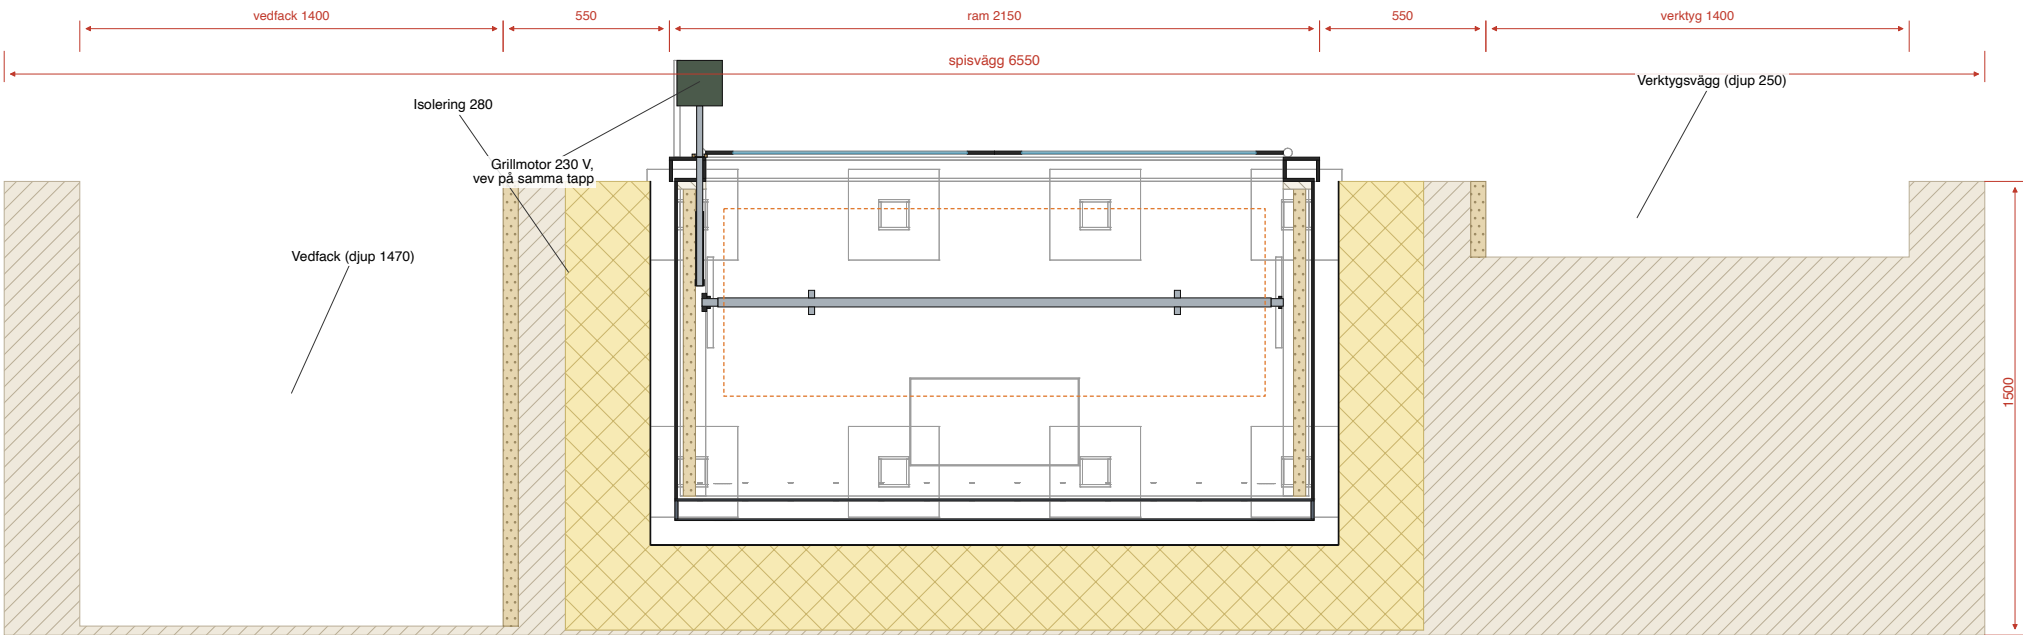

E–E plan genom takvingarnas vattenspalt (z = 2186)

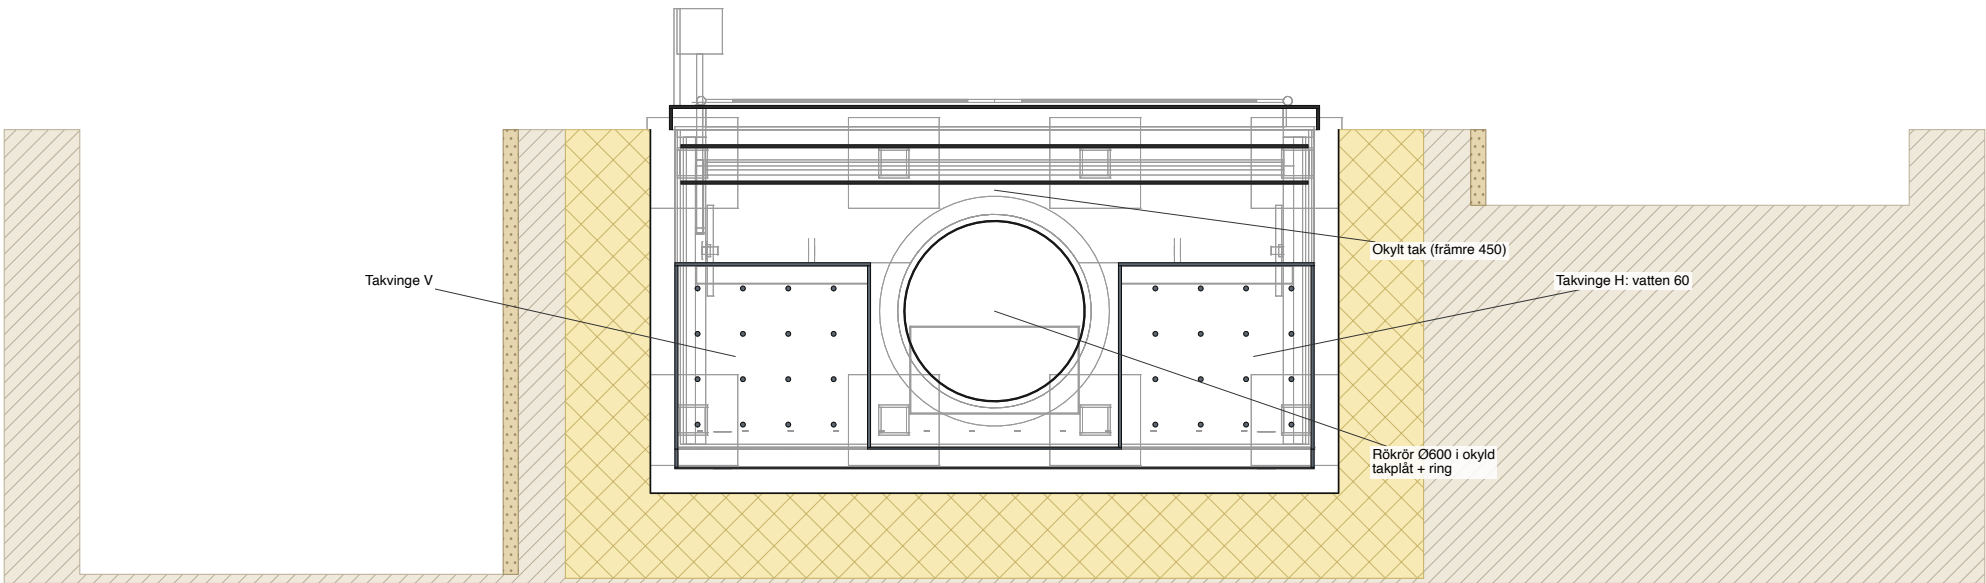


Snitt C–C och E–E · plan

C: i spetthöjd (z = 1200) · E: genom takvingarnas vattenspalt (z = 2186)

Skala 1:25 (A3)

Garibaldi · Hugo Ljungberg · 2026-10-10 · mm

Blad 3 / 6

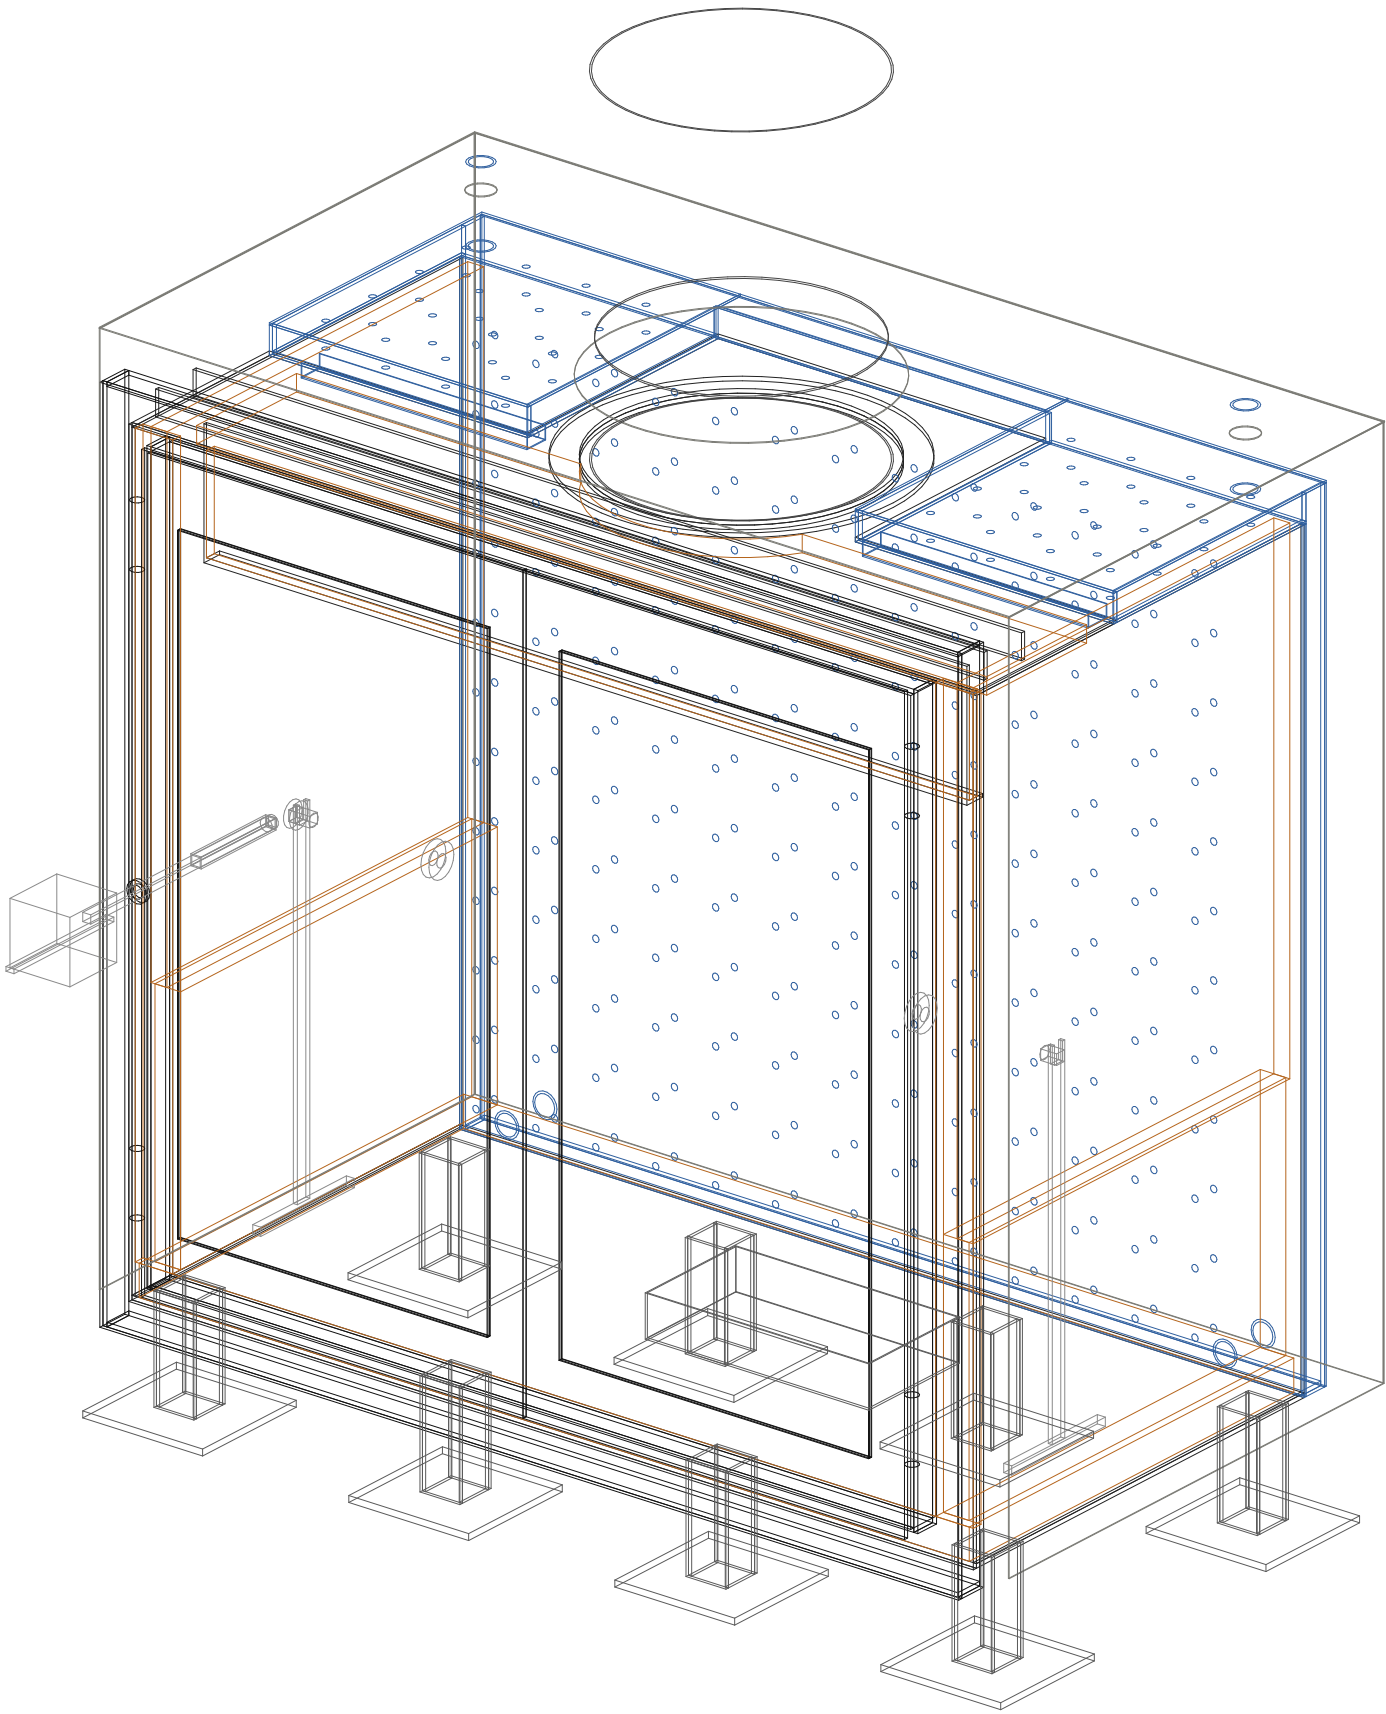

- Eldstadslåda
- Vattenmantel + stag
- Front och luckor
- Infodring
- Spett och drivning
- Konvektionsmantel
- Rökrör
- Ben och golv

Vikter ur modellen (kg)

Eldstadslåda	624
Vattenmantel + stag	496
Front och luckor	277
Infodring	550
Spett och drivning	27
Konvektionsmantel	190
Rökrör	58
Ben och golv	139
Stål totalt	1811
Infodring	550
Vatten (ca 290 l)	290
I drift ≈ 2651 kg	



Axonometri · wireframe

Hela insatsen, färg per komponent (referenser dolda)

Skala ingen (A3)

Garibaldi · Hugo Ljungberg · 2026-10-10 · mm

Blad 4 / 6

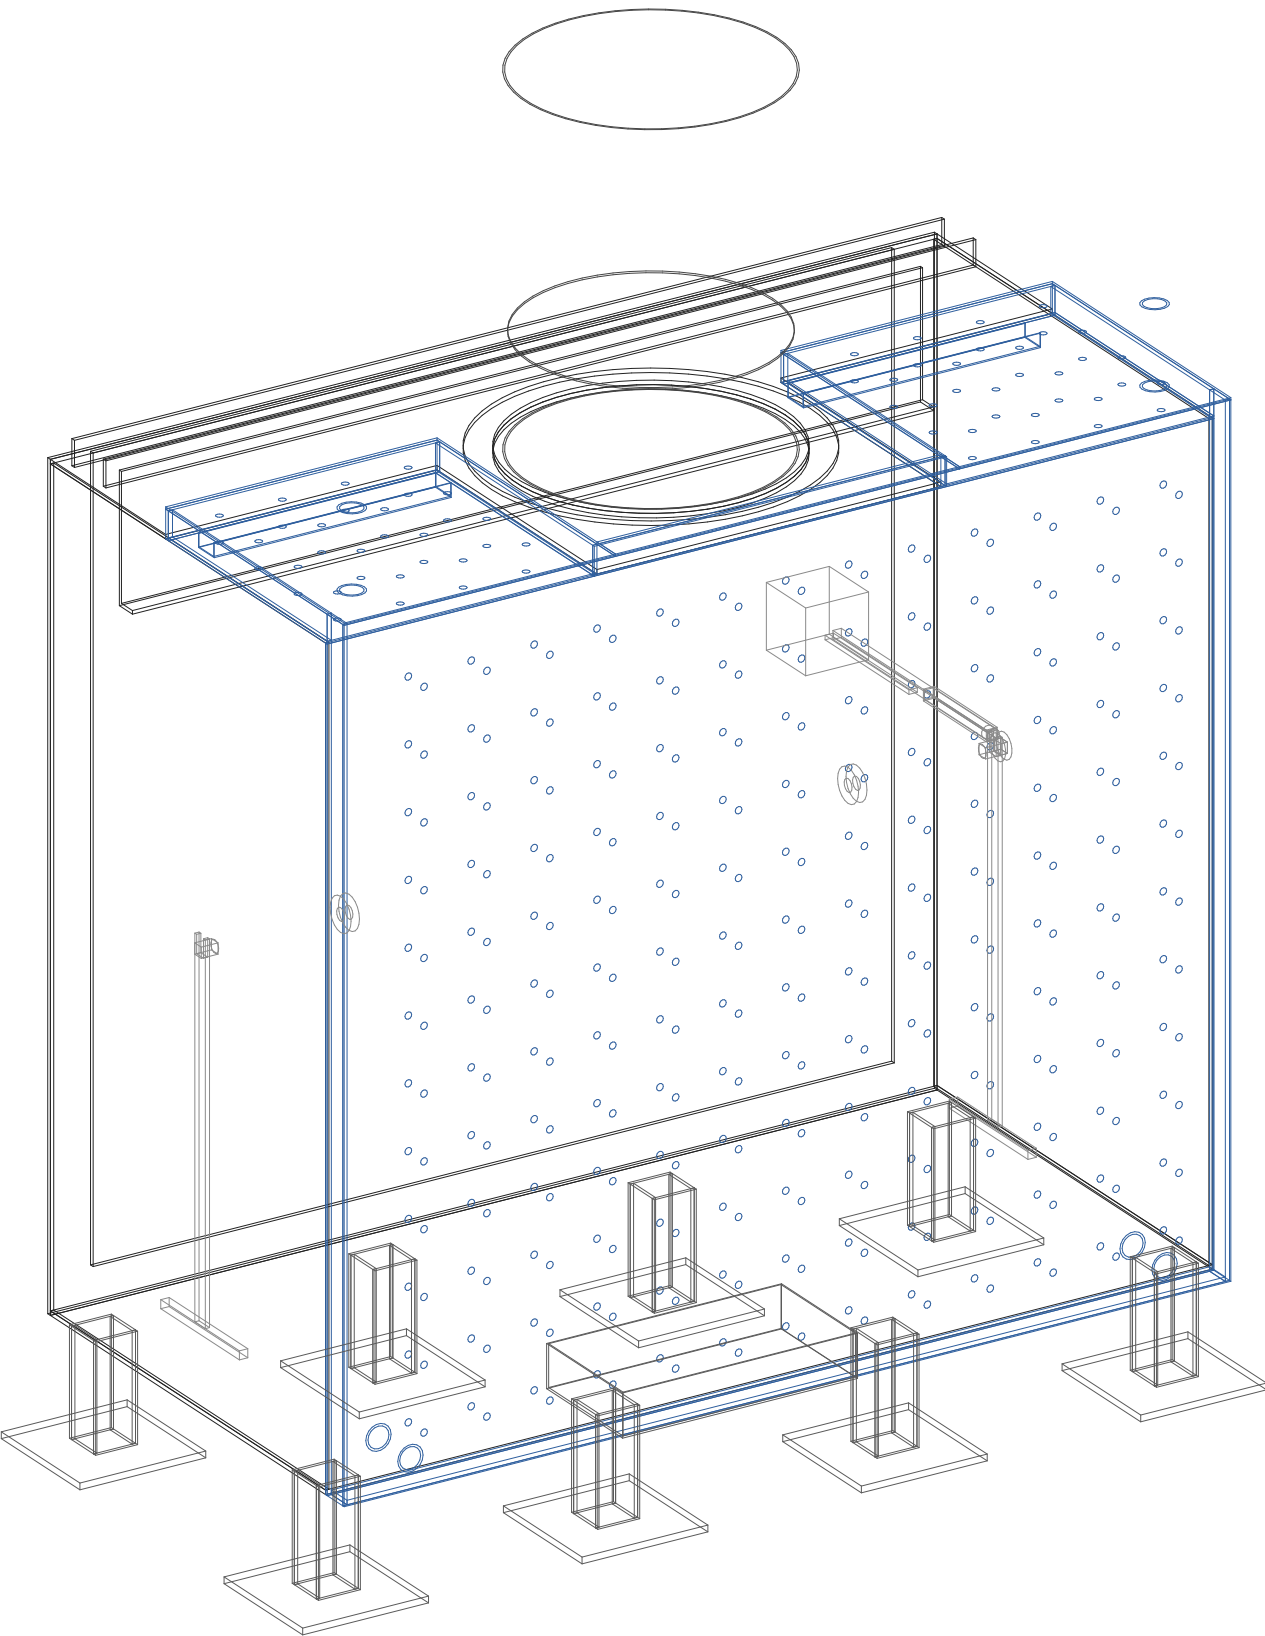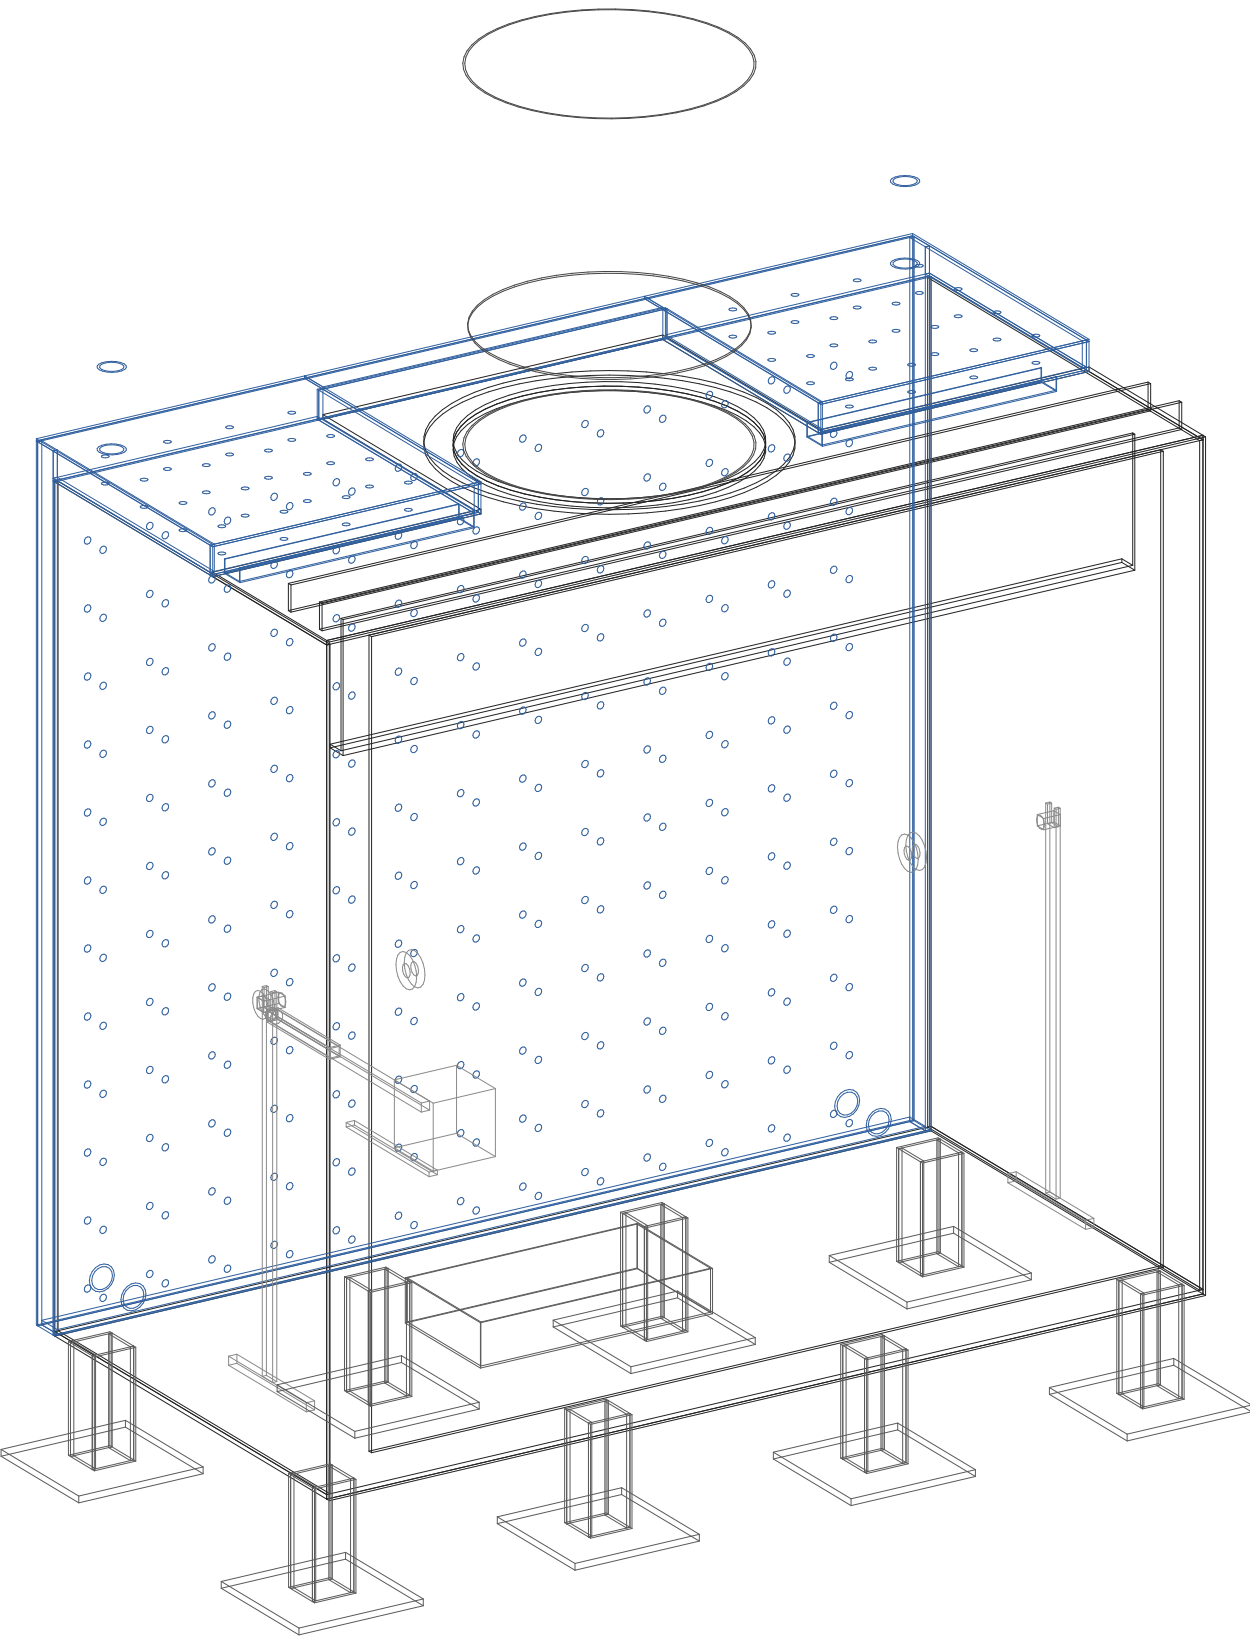

Axonometri · wireframe, inre delar

Vänster: utan front, konvektionsmantel och infodring · Höger: bakifrån (vattenmantel) Skala ingen (A3)

Garibaldi · Hugo Ljungberg · 2026-10-10 · mm

Blad 5 / 6

OppB	1910 mm = 1910 mm · Eldstadsopkning bredd
OppH	1800 mm = 1800 mm · Eldstadsopkning hojd
Sill	350 mm = 350 mm · Oppningens underkant over salgolv
LadaD	1050 mm = 1050 mm · Eldstadsdjup, oppningsplan till bakmantel
TegelT	64 mm = 64 mm · Eldfast tegel
Bruk	10 mm = 10 mm · Eldfast bruk under golvtegel
InfSpalt	30 mm = 30 mm · Spalt tegel-stal sidor
TegelH	600 mm = 600 mm · Tegelzon pa sidorna
VermT	40 mm = 40 mm · Vermiculit
FiberT	25 mm = 25 mm · Keramisk fiber
LadaB	OppB + 2 * (TegelT + InfSpalt) = 2098 mm · Ladans innerbredd (fri bredd mellan tegel = OppB)
ZB	Sill – TegelT – Bruk = 276 mm · Stalbottnens ovansida
ZR	Sill + OppH = 2150 mm · Takets undersida
PlSida	8 mm = 8 mm · Sidovaggar
PlBotten	10 mm = 10 mm · Botten
PlTak	10 mm = 10 mm · Okyld takplat
XO	LadaB / 2 + PlSida = 1057 mm · Ladans yttre halvbredd
Mantellnre	6 mm = 6 mm · Mantelplat mot eld
MantelSpalt	60 mm = 60 mm · Vattenspalt
MantelYttre	5 mm = 5 mm · Yttre mantelplat
MantelKant	10 mm = 10 mm · Kantplattstang
VingeD	600 mm = 600 mm · Vattenkyld takzon baktill
RorD	600 mm = 600 mm · Rokror
RorFranBak	450 mm = 450 mm · Rokrorets centrum fran bakmantel
RingB	60 mm = 60 mm · Forstarkningsring bredd
VingeX0	RorD / 2 + 20 mm + RingB + 40 mm = 420 mm · Takvingarnas inre kant
StagCC	150 mm = 150 mm · Stag c/c

StagD	16 mm = 16 mm · Stag diameter
RamProfil	120 mm = 120 mm · Ramens bredd runt oppningen
RamT	10 mm = 10 mm · Ramplat
RamUt	80 mm = 80 mm · Ram framfor spisvaggen
LuckaT	10 mm = 10 mm · Luckplat
GlasKant	90 mm = 90 mm · Luckans ram runt glaset
RokplatH	300 mm = 300 mm · Rokplat hojd
RokplatIn	100 mm = 100 mm · Rokplat innanfor front
RokplatT	8 mm = 8 mm · Rokplat tjocklek
RokplatKant	50 mm = 50 mm · Bockad kant
SpettY	400 mm = 400 mm · Spett fran front (300/400/500)
SpettZ	850 mm = 850 mm · Spett over eldstadsgolvet (650-1050)
SpettD	30 mm = 30 mm · Spett diameter
KonvSpalt	80 mm = 80 mm · Konvektionsspalt sidor/bak
KonvSpaltTak	120 mm = 120 mm · Konvektionsspalt over tak
KonvT	2 mm = 2 mm · Konvektionsmantel
Iso	280 mm = 280 mm · Skikt 4-9 utanfor konvektionsmanteln
VaggT	1500 mm = 1500 mm · Spisvagg tjocklek
VaggB	6550 mm = 6550 mm · Spisvagg bredd
VaggH	3000 mm = 3000 mm · Spisvagg hojd
FackAvst	550 mm = 550 mm · Fack fran ramens kant
FackB	1400 mm = 1400 mm · Fackbredd
FackIso	50 mm = 50 mm · Kalciumsilikat fack-insats
BenFri	50 mm = 50 mm · Fri hojd under ladan (ben)

Parametrar (Fusion)	
Modify > Change Parameters · alla mått härleds härifrån	Skala – (A3)
Garibaldi · Hugo Ljungberg · 2026-10-10 · mm	Blad 6 / 6